
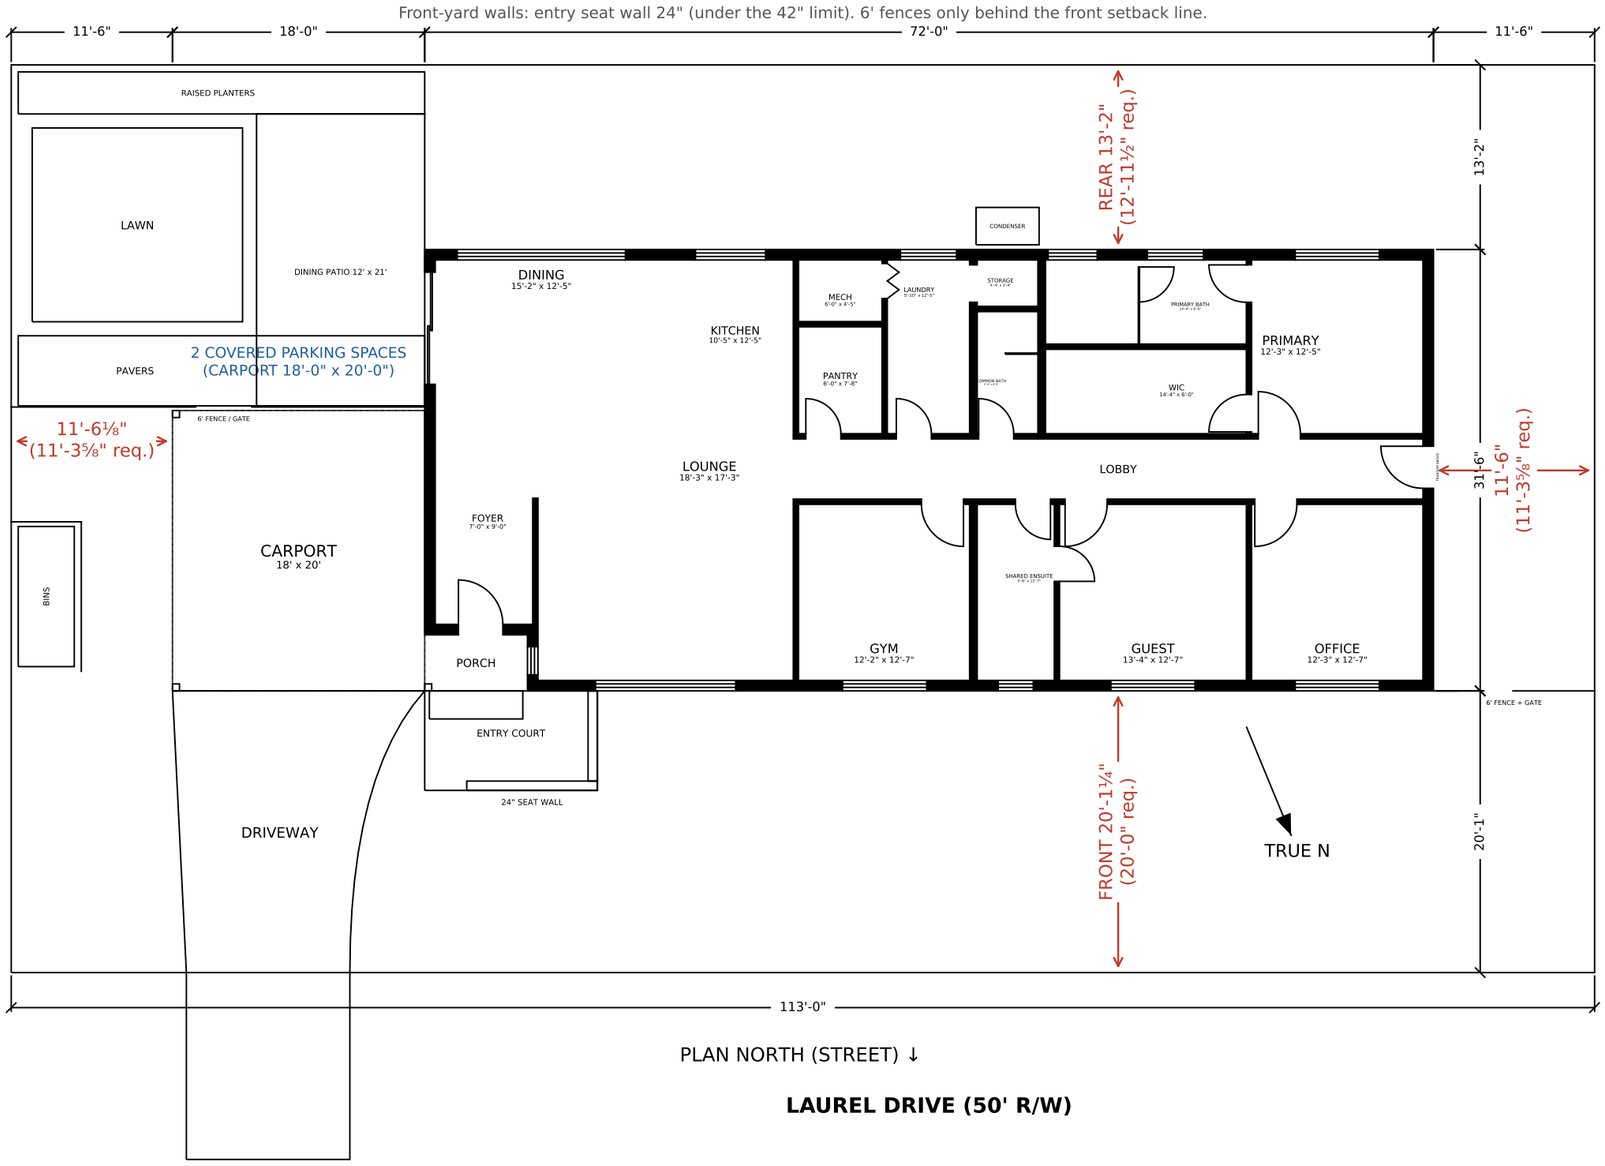


PROJECT DATA

Scope	Non-like-for-like rebuild, 1-story SFR + attached carport (Eaton Fire)
Zone / overlay	R-1 · Altadena CSD · VHFHSZ
Lot	113.00' x 64.77' = 7,319 sq ft
Floor area (to outside of walls)	2,238 sq ft
Covered porch	29 sq ft
Carport (attached, open)	360 sq ft
Lot coverage	2,628 sq ft (35.9%)
CSD limit (¼ lot + 1,000)	2,830 sq ft (coverage and floor area)
Stories / max height	1 story · ~17'-7" above finished floor (top of roof at the street eave)
Bedrooms / baths	4 / 3
Parking	2 covered (carport)

SETBACKS	required · provided
Front (street)	20'-0" · 20'-1¼"
Rear	12'-11½" · 13'-2"
Side, west	11'-3⅝" · 11'-6"
Side, east (carport)	11'-3⅝" · 11'-6⅛"
Glazing (Title 24 check)	~448 sq ft (~20.0% of floor)

NOTES
1. Setbacks measured to the outside face of exterior walls (eaves excluded).
2. Side setback taken as 10% of lot width; rear as 20% of lot depth. Please confirm.
3. Heights are above finished floor; the lot falls ~4' across the footprint, so height above grade depends on the foundation design (to be set with the civil).
4. Existing retaining wall and chimney (survey) to be removed.
5. Survey: topographic survey on file (APN above).

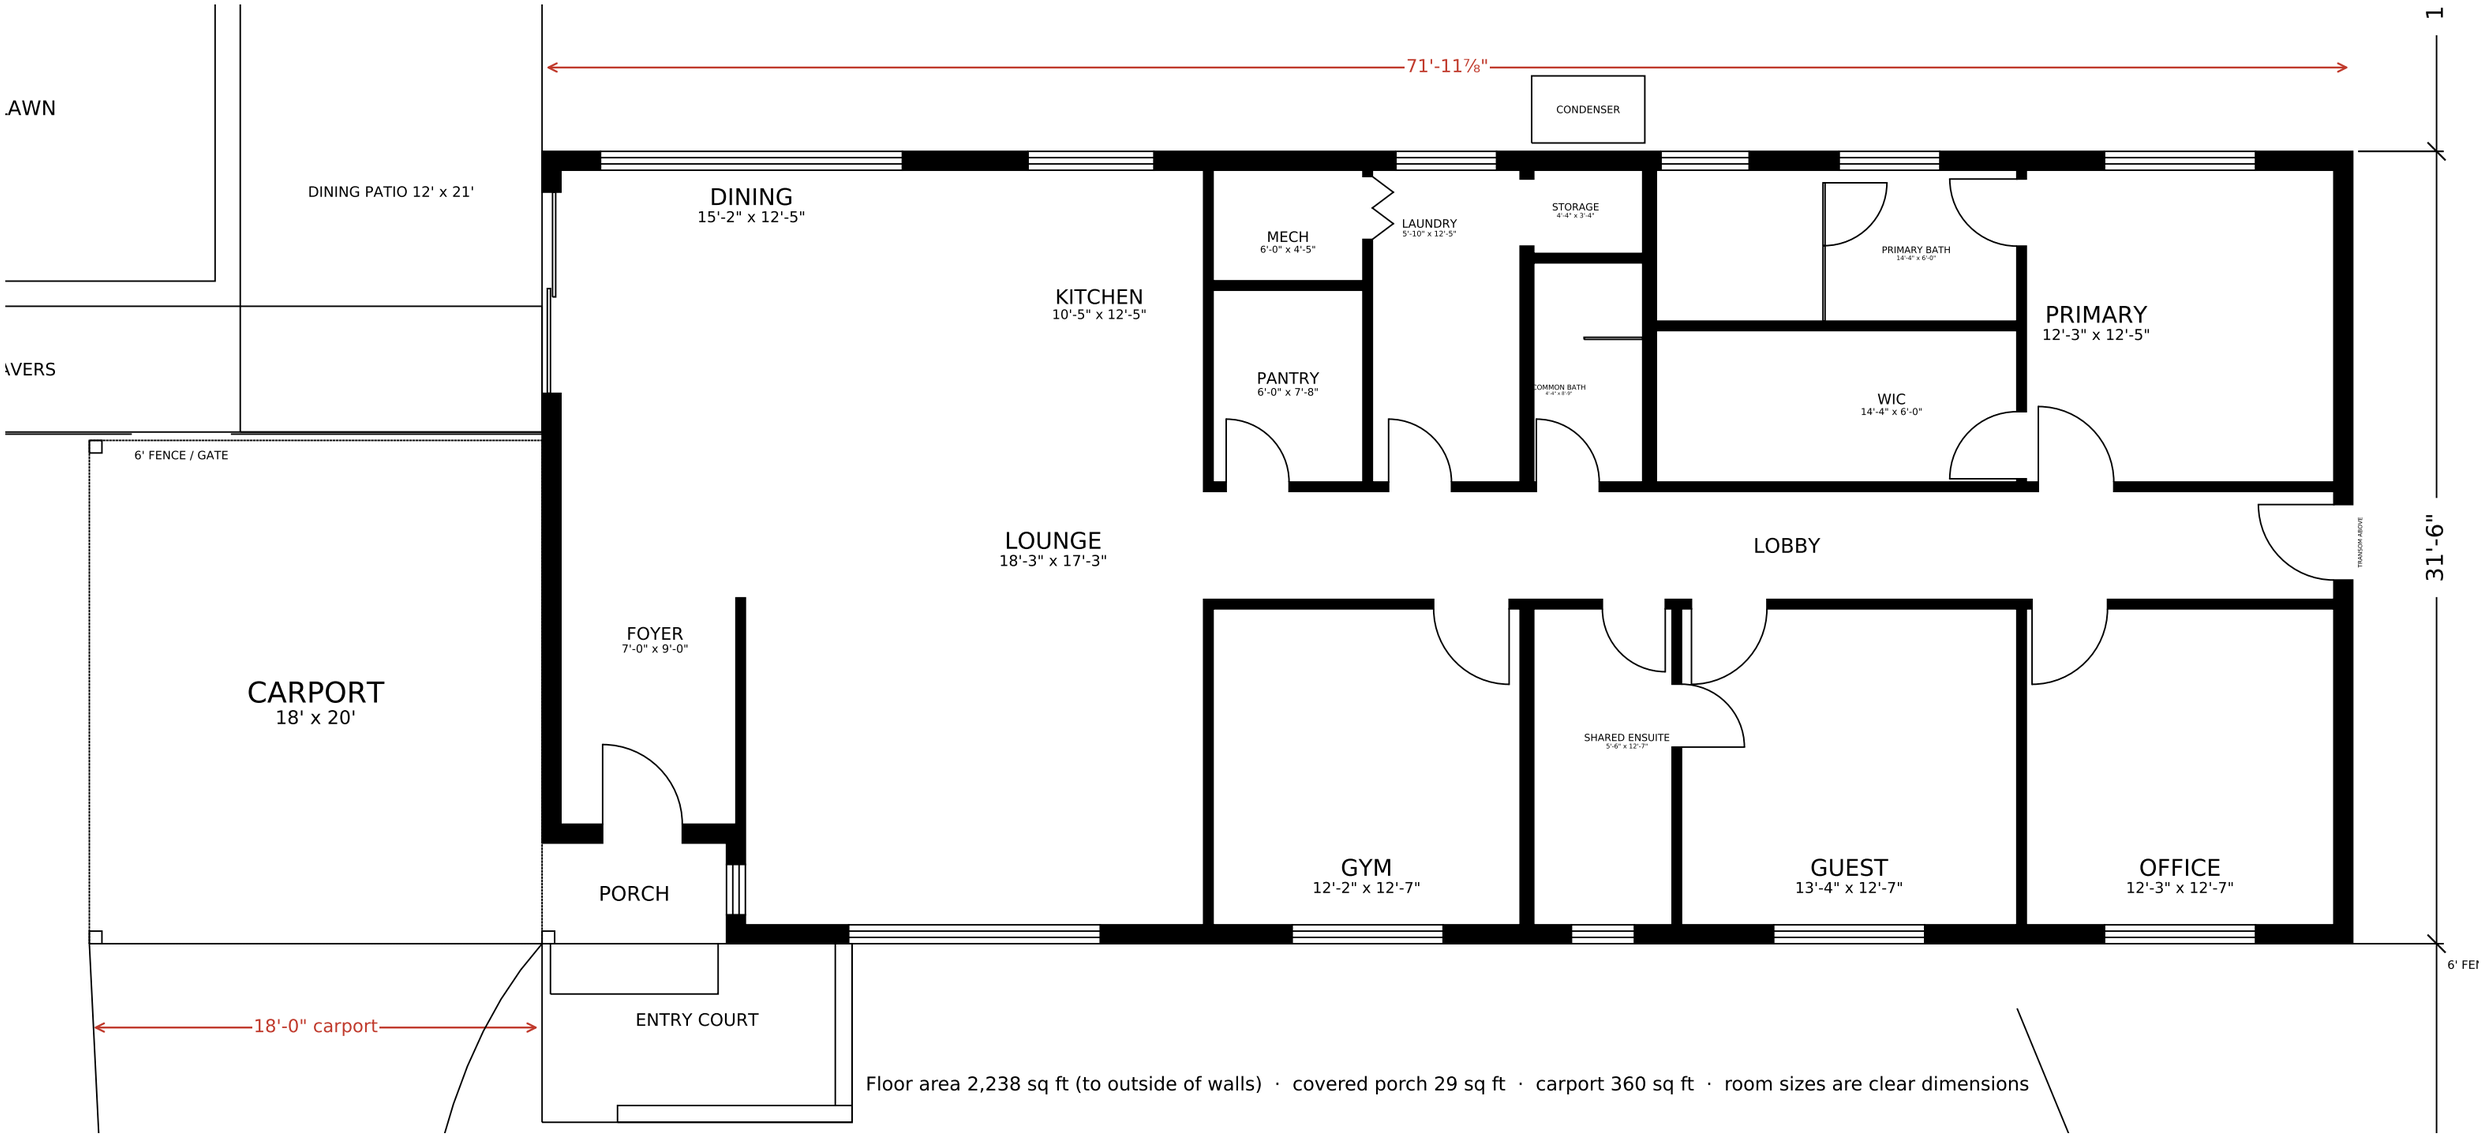

Floor area 2,238 sq ft (to outside of walls) · covered porch 29 sq ft · carport 360 sq ft · room sizes are clear dimensions


Single-family residence rebuild (Eaton Fire), 220 Laurel Dr, Altadena CA 91001

APN 5832-003-027 · Zone R-1, Altadena Community Standards District · Owner: Richard Acosta

PRELIMINARY ZONING CHECK SET — OWNER-PREPARED, NOT FOR CONSTRUCTION

October 15, 2026 · Dimensions in feet-inches · Plan north = street side

Floor plan & areas **Z-2**

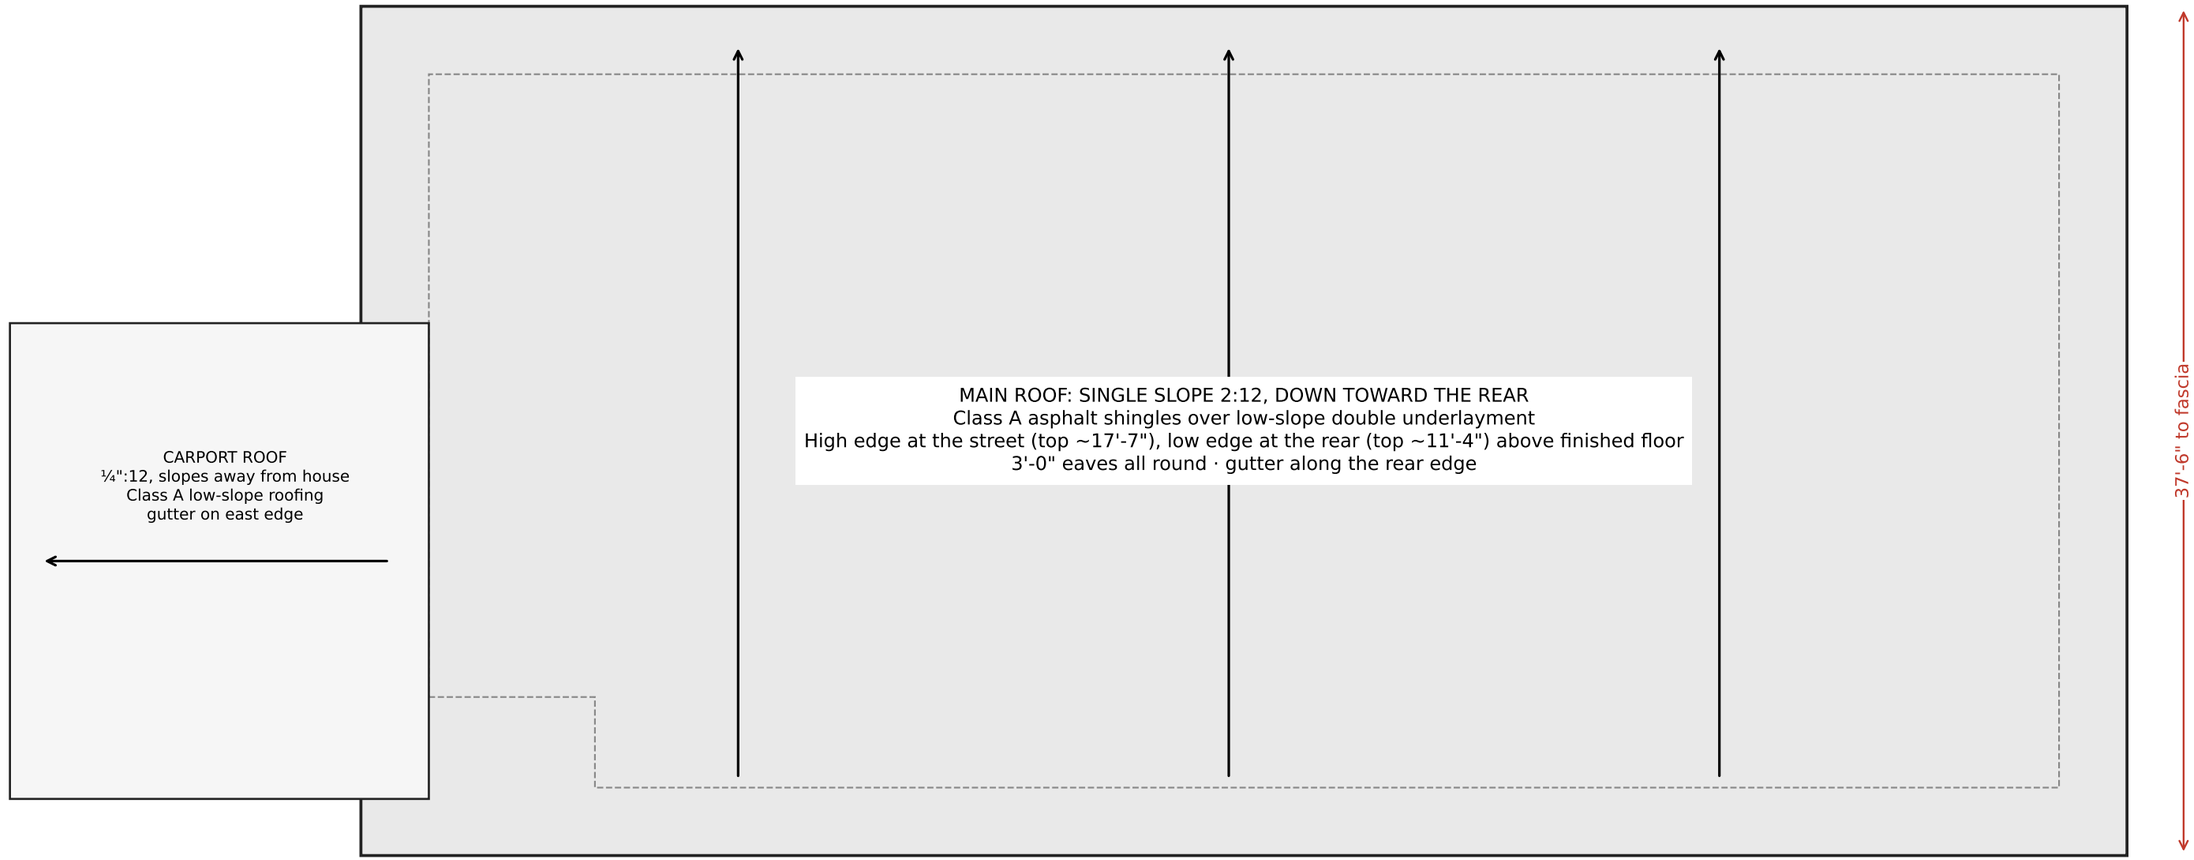

Single-family residence rebuild (Eaton Fire), 220 Laurel Dr, Altadena CA 91001

APN 5832-003-027 · Zone R-1, Altadena Community Standards District · Owner: Richard Acosta


PRELIMINARY ZONING CHECK SET — OWNER-PREPARED, NOT FOR CONSTRUCTION

October 15, 2026 · Dimensions in feet-inches · Plan north = street side


Roof plan **Z-3**

Heights above finished floor. The lot falls ~4' across the footprint (survey); grade lines and height above grade to follow the foundation/grading design.


NORTH (STREET) ELEVATION

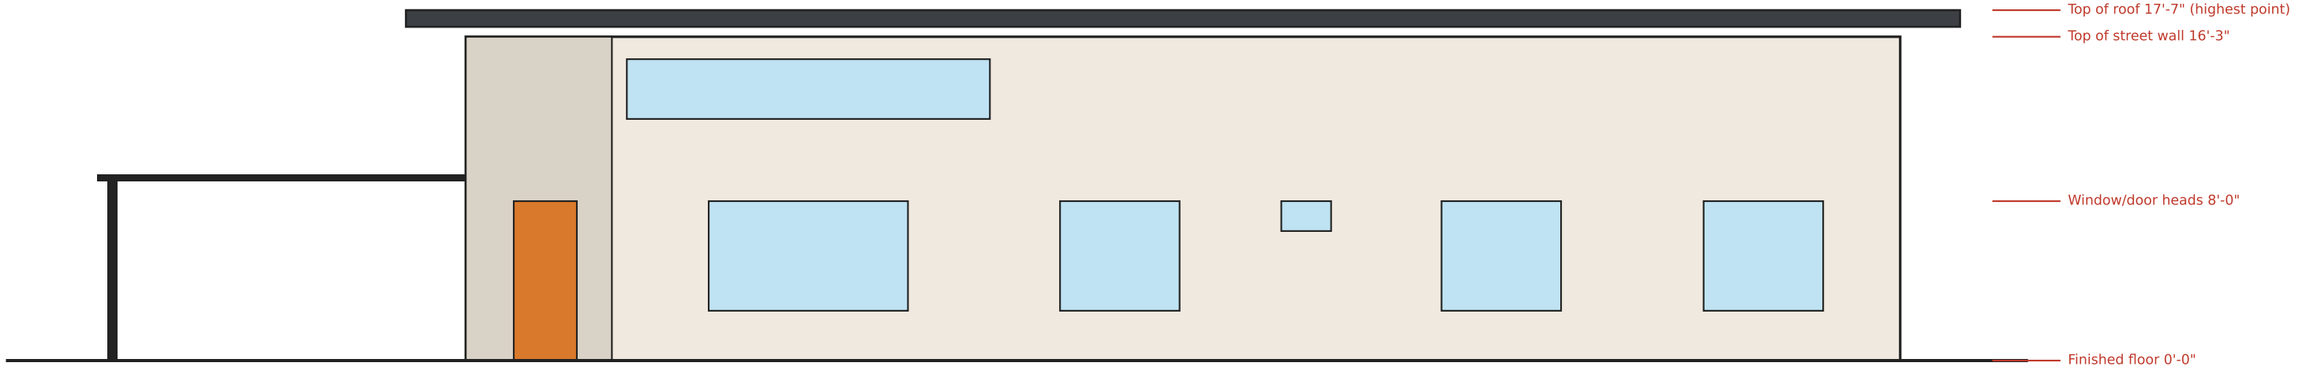

SOUTH (REAR) ELEVATION

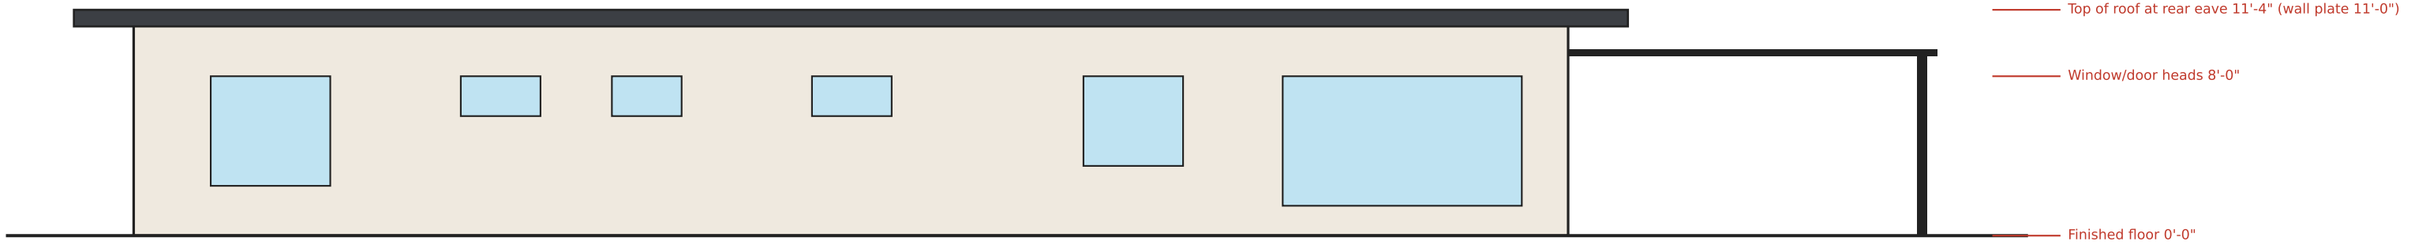

EAST (CARPORT) ELEVATION

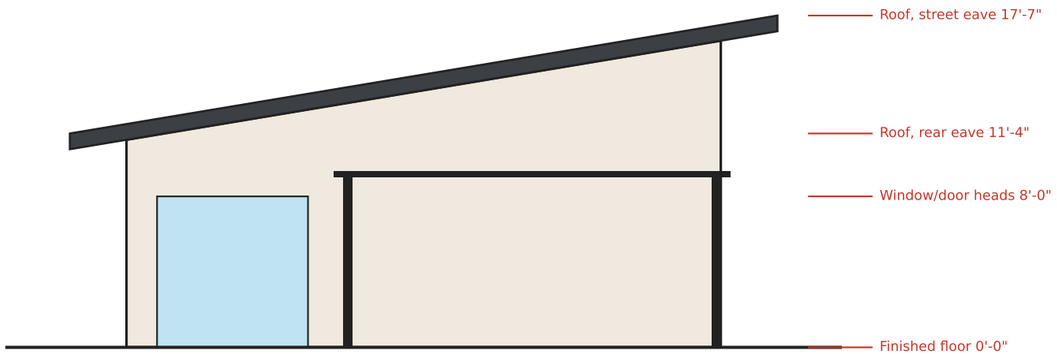

WEST ELEVATION

