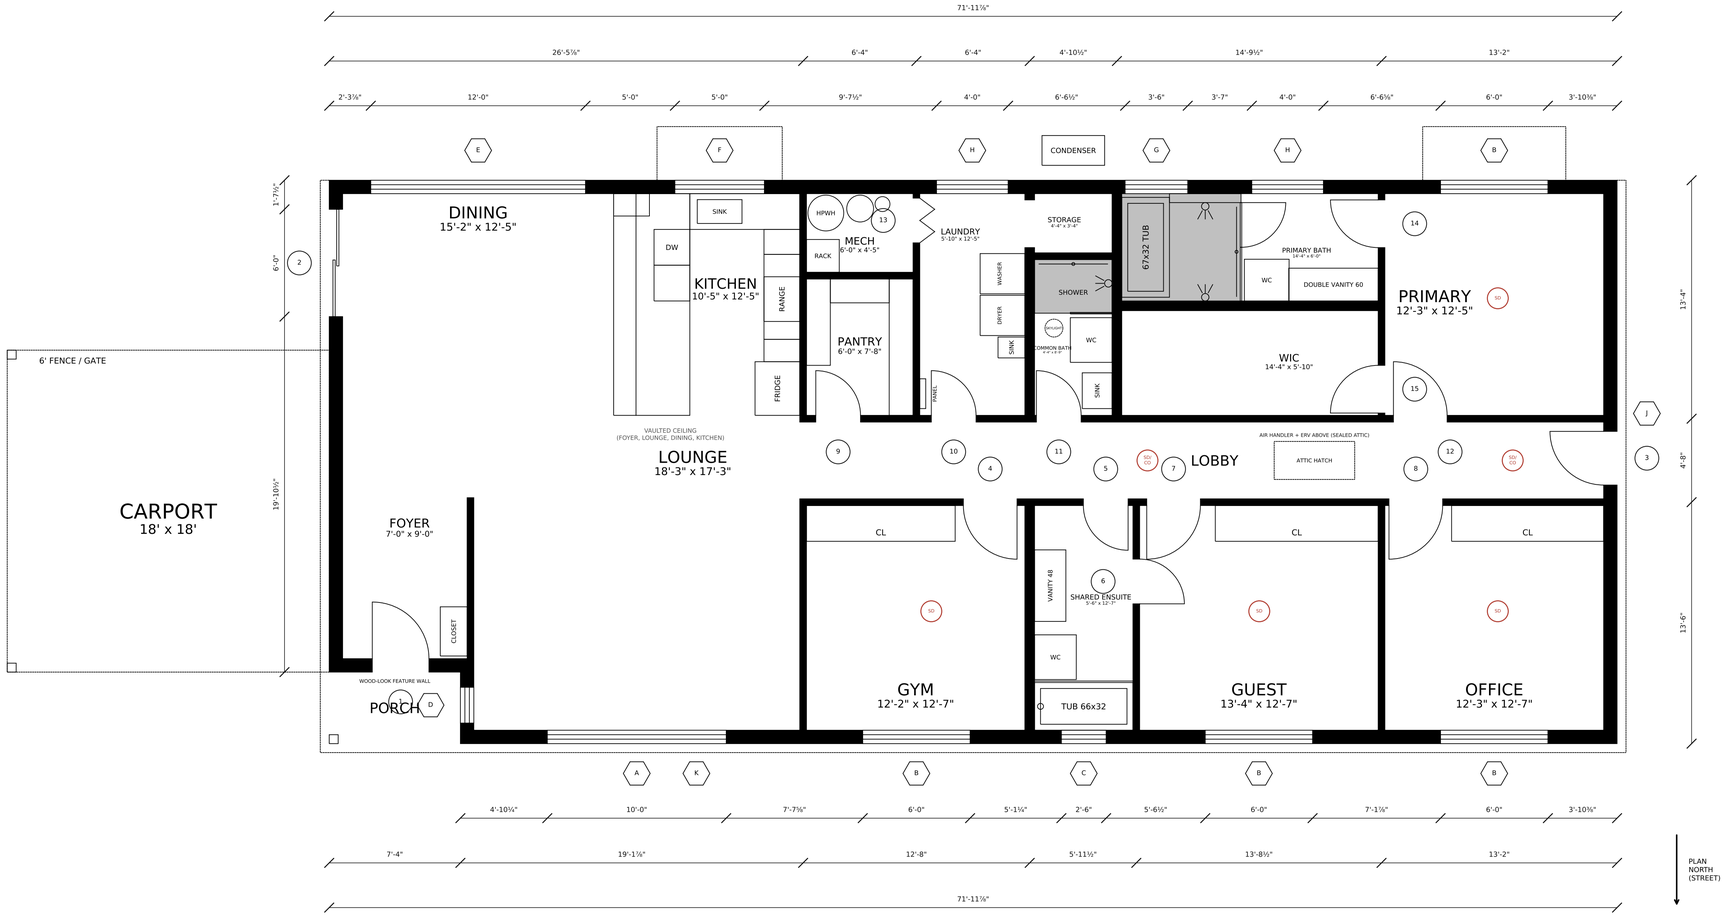



**FLOOR PLAN 1/4" = 1'-0"**

GENERAL NOTES

1. Dimensions are to wall centrelines; exterior walls to the outside face of framing + finish (9" walls).
2. Walls: exterior 2x6 with 1" rigid insulation and stucco; interior 2x4; plumbing walls 2x6.
3. Ceilings 9'-0" unless noted. The foyer, lounge, dining and kitchen are vaulted under the roof (see sections).
4. Doors 8'-0" high unless noted. Exterior doors and glazing per CRC R337 (VHFHSZ).
5. All exterior glazing dual-pane with at least one tempered pane (CRC R337.8.2.1). Fully tempered where noted (CRC R308.4).
6. Bedroom windows meet emergency escape: 5.7 sq ft net clear, 20" min width, 24" min height, sill 44" max (CRC R310).
7. Smoke alarms in each bedroom and outside the sleeping areas, hard-wired, interconnected, battery backup, at least 3' from bathroom doors (CRC R314). Outside the sleeping areas: combination smoke / CO alarms (CO not required in an all-electric house with no attached garage, CRC R315.2; provided anyway).
8. All-electric: heat pump HVAC (air handler and ERV in the sealed attic; outdoor unit at the rear wall), heat pump water heater (HPWH) in the mechanical closet.
9. Fire sprinklers throughout (NFPA 13D); plans by the sprinkler designer (deferred submittal).
10. Attic access: 22" x 54" pull-down ladder in the hall, 30" min headroom above (CRC R807.1).
11. Furniture not shown; closets, cabinets and fixtures shown for reference.

## DOOR SCHEDULE

| TAG | LOCATION | SIZE (W x H) | TYPE | NOTES |
|---|---|---|---|---|
| 1 | PORCH / FOYER (exterior) | 3'-2" x 8'-0" | Hinged | Solid core 1-3/8"+ or noncombustible (CRC R337.8.3); weatherstripped |
| 2 | DINING (exterior) | 6'-0" x 8'-0" | Sliding glass door | Solid core 1-3/8"+ or noncombustible (CRC R337.8.3); weatherstripped; dual-pane tempered glazing |
| 3 | LOBBY (exterior) | 3'-0" x 7'-0" | Hinged, half-lite | Solid core 1-3/8"+ or noncombustible (CRC R337.8.3); weatherstripped; dual-pane tempered glazing; 3'-0" x 1'-6" transom above (window J) |
| 4 | GYM / LOBBY | 3'-0" x 8'-0" | Hinged | |
| 5 | SHARED ENSUITE / LOBBY | 2'-6" x 8'-0" | Hinged | privacy lock |
| 6 | SHARED ENSUITE / GUEST | 2'-6" x 8'-0" | Hinged | privacy lock |
| 7 | GUEST / LOBBY | 3'-0" x 8'-0" | Hinged | |
| 8 | OFFICE / LOBBY | 3'-0" x 8'-0" | Hinged | |
| 9 | LOUNGE / PANTRY | 2'-6" x 8'-0" | Hinged | |
| 10 | LOUNGE / LAUNDRY | 2'-6" x 8'-0" | Hinged | solid core (noise) |
| 11 | LOBBY / COMMON BATH | 2'-6" x 8'-0" | Hinged | privacy lock; solid core (noise) |
| 12 | LOBBY / PRIMARY | 3'-0" x 8'-0" | Hinged | |
| 13 | MECH / LAUNDRY | 2'-6" x 8'-0" | Bifold, louvered | solid core (noise); louvered for the water heater's air |
| 14 | PRIMARY BATH / PRIMARY | 2'-8" x 8'-0" | Hinged | privacy lock |
| 15 | WIC / PRIMARY | 2'-8" x 8'-0" | Hinged | |

## WINDOW SCHEDULE

| TAG | QTY | LOCATION | SIZE (W x H) | SILL | OPERATION | NOTES |
|---|---|---|---|---|---|---|
| A | 1 | Lounge | 10'-0" x 5'-6" | 2'-6" | Fixed center, slider each end | |
| B | 4 | Gym, Guest, Office, Primary | 6'-0" x 5'-6" | 2'-6" | Horizontal slider | Emergency escape (CRC R310): one sash opens ~2'-9" x 5'-3", over 5.7 sq ft net clear; sill under 44" |
| C | 1 | Shared Ensuite | 2'-6" x 1'-6" | 6'-6" | Awning | Above the tub; bottom edge over 60" above it, so tempering not required (CRC R308.4.5); obscure glass |
| D | 1 | Foyer | 2'-0" x 5'-6" | 2'-6" | Fixed, reeded glass | Tempered: within 24" of the front door (CRC R308.4.2) |
| E | 1 | Dining | 12'-0" x 6'-6" | 1'-6" | Fixed, two units mulled | Tempered: within 24" of the dining slider (CRC R308.4.2) |
| F | 1 | Kitchen | 5'-0" x 4'-6" | 3'-6" | Horizontal slider | Over the sink |
| G | 1 | Primary Bath | 3'-6" x 2'-0" | 6'-0" | Awning | Above the tub; bottom edge over 60" above it, so tempering not required (CRC R308.4.5) |
| H | 2 | Laundry, Primary Bath | 4'-0" x 2'-0" | 6'-0" | Awning | High window |
| J | 1 | Lobby | 3'-0" x 1'-6" | 7'-2" | Fixed transom | Above the door; bottom edge over 60" (not a hazardous location) |
| K | 1 | Lounge | 18'-2⅛" x 3'-0" | 12'-1½" | Fixed (mulled units) | Clerestory over the lounge |

## LEGEND

- (1) Door tag (see door schedule)
- (A) Window tag (see window schedule)
- (SD) Smoke alarm (SD), smoke / CO alarm (SD/CO)
- Overhead: band, canopy, attic hatch, skylight

# ACOSTA RESIDENCE

Single-family residence
fire rebuild (Eaton Fire)

220 Laurel Dr
Altadena, CA 91001
APN 5832-003-027

Zone R-1 · Altadena CSD
Very High Fire Hazard Severity Zone

Owner: Richard Acosta

Prepared by: _____

Structural: by engineer (separate sheets)

**DRAFT FOR REVIEW not for construction**

Date: October 15, 2026
Revisions:

© 2026 Richard Acosta. All rights reserved. These drawings are for 220 Laurel Dr only. Not to be copied, adapted, sold or built from on any other site.

**FLOOR PLAN, DOOR & WINDOW SCHEDULES**

**A-2**