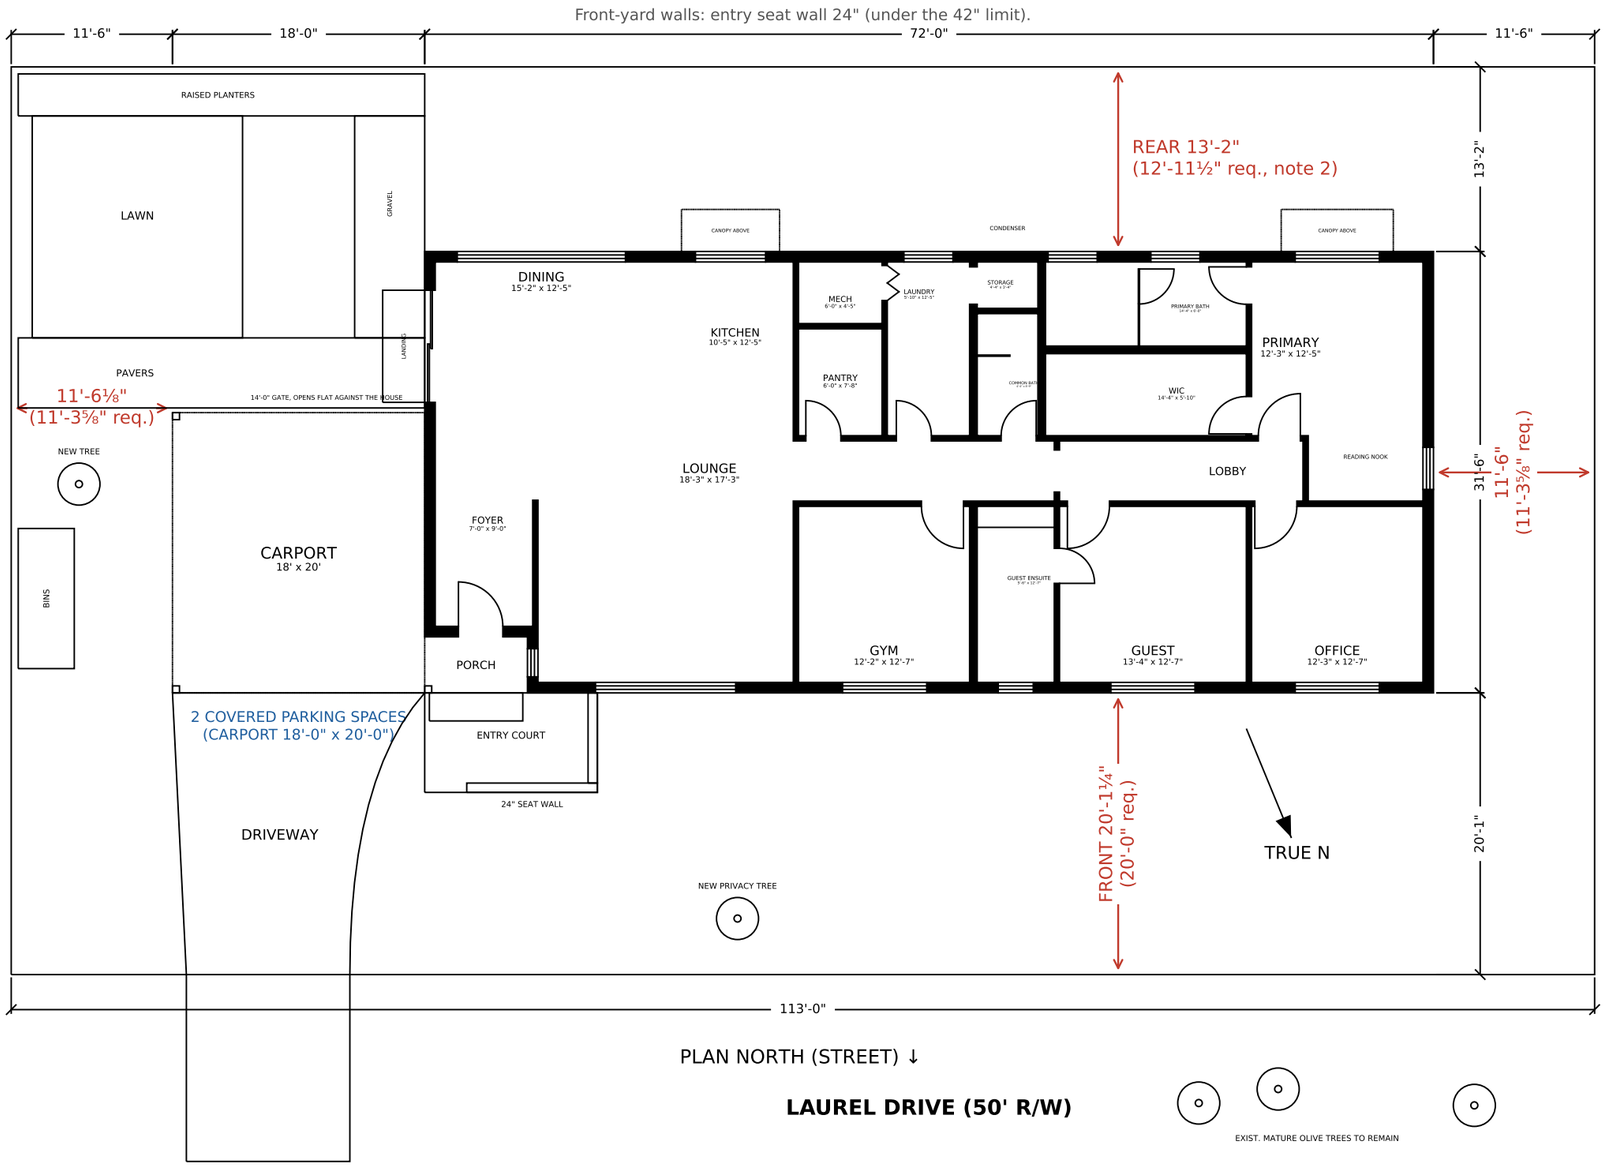



## PROJECT DATA

| | |
|---|---|
| Scope | Non-like-for-like rebuild, 1-story SFR + attached carport (Eaton Fire) |
| Zone / overlay | R-1 · Altadena CSD · VHFHSZ |
| Lot | 113.00' x 64.77' = 7,319 sq ft |
| Floor area (to outside of walls) | 2,238 sq ft |
| Covered porch | 29 sq ft |
| Carport (attached, open) | 360 sq ft |
| Lot coverage | 2,628 sq ft (35.9%) |
| CSD limit (¼ lot + 1,000) | 2,830 sq ft (coverage and floor area) |
| Stories / max height | 1 story · ~17'-6" above finished floor (top of roof at the street eave) |
| Bedrooms / baths | 4 / 3 |
| Parking | 2 covered (carport) |

| **SETBACKS** | required · provided |
|---|---|
| Front (street) | 20'-0" · 20'-1¼" |
| Rear (§22.110.080.D) | 12'-11½" · 13'-2" |
| Side, west | 11'-3⅝" · 11'-6" |
| Side, east (carport) | 11'-3⅝" · 11'-6⅛" |
| Glazing (Title 24 check) | ~453 sq ft (~20.2% of floor) |

NOTES
1. Setbacks measured to the outside face of exterior walls (eaves excluded).
2. Side setback taken as 10% of lot width. Rear yard on a shallow lot (§22.110.080.D): the lot is 64.77' deep (under 75'), so the rear yard is 20% of the average depth, 12'-11½". Please confirm it applies under the Altadena CSD.
3. Heights are above finished floor; the lot falls ~4' across the footprint, so height above grade depends on the foundation design (to be set with the civil).
4. Lot lines, lot dimensions and existing trees are from the owner's topographic survey (available on request).
5. Eaves 2'-6" all round: the most an eave may project into a required yard (§22.110.090.A); more than 2'-6" from every lot line, no supports in the yards.
6. Rear window canopies 3'-0" deep (§22.110.090.B: up to 5' into the rear yard): over the windows only, 1' past each side, no supports in the yard.

**Single-family residence rebuild (Eaton Fire), 220 Laurel Dr, Altadena CA 91001**


APN 5832-003-027 · Zone R-1, Altadena Community Standards District · Owner: Richard Acosta

PRELIMINARY ZONING CHECK SET — OWNER-PREPARED, NOT FOR CONSTRUCTION

October 15, 2026 · Dimensions in feet-inches · Plan north = street side

Site plan & project data **Z-1**

© 2026 Richard Acosta. All rights reserved. For 220 Laurel Dr only: not to be copied, adapted or built from anywhere else.

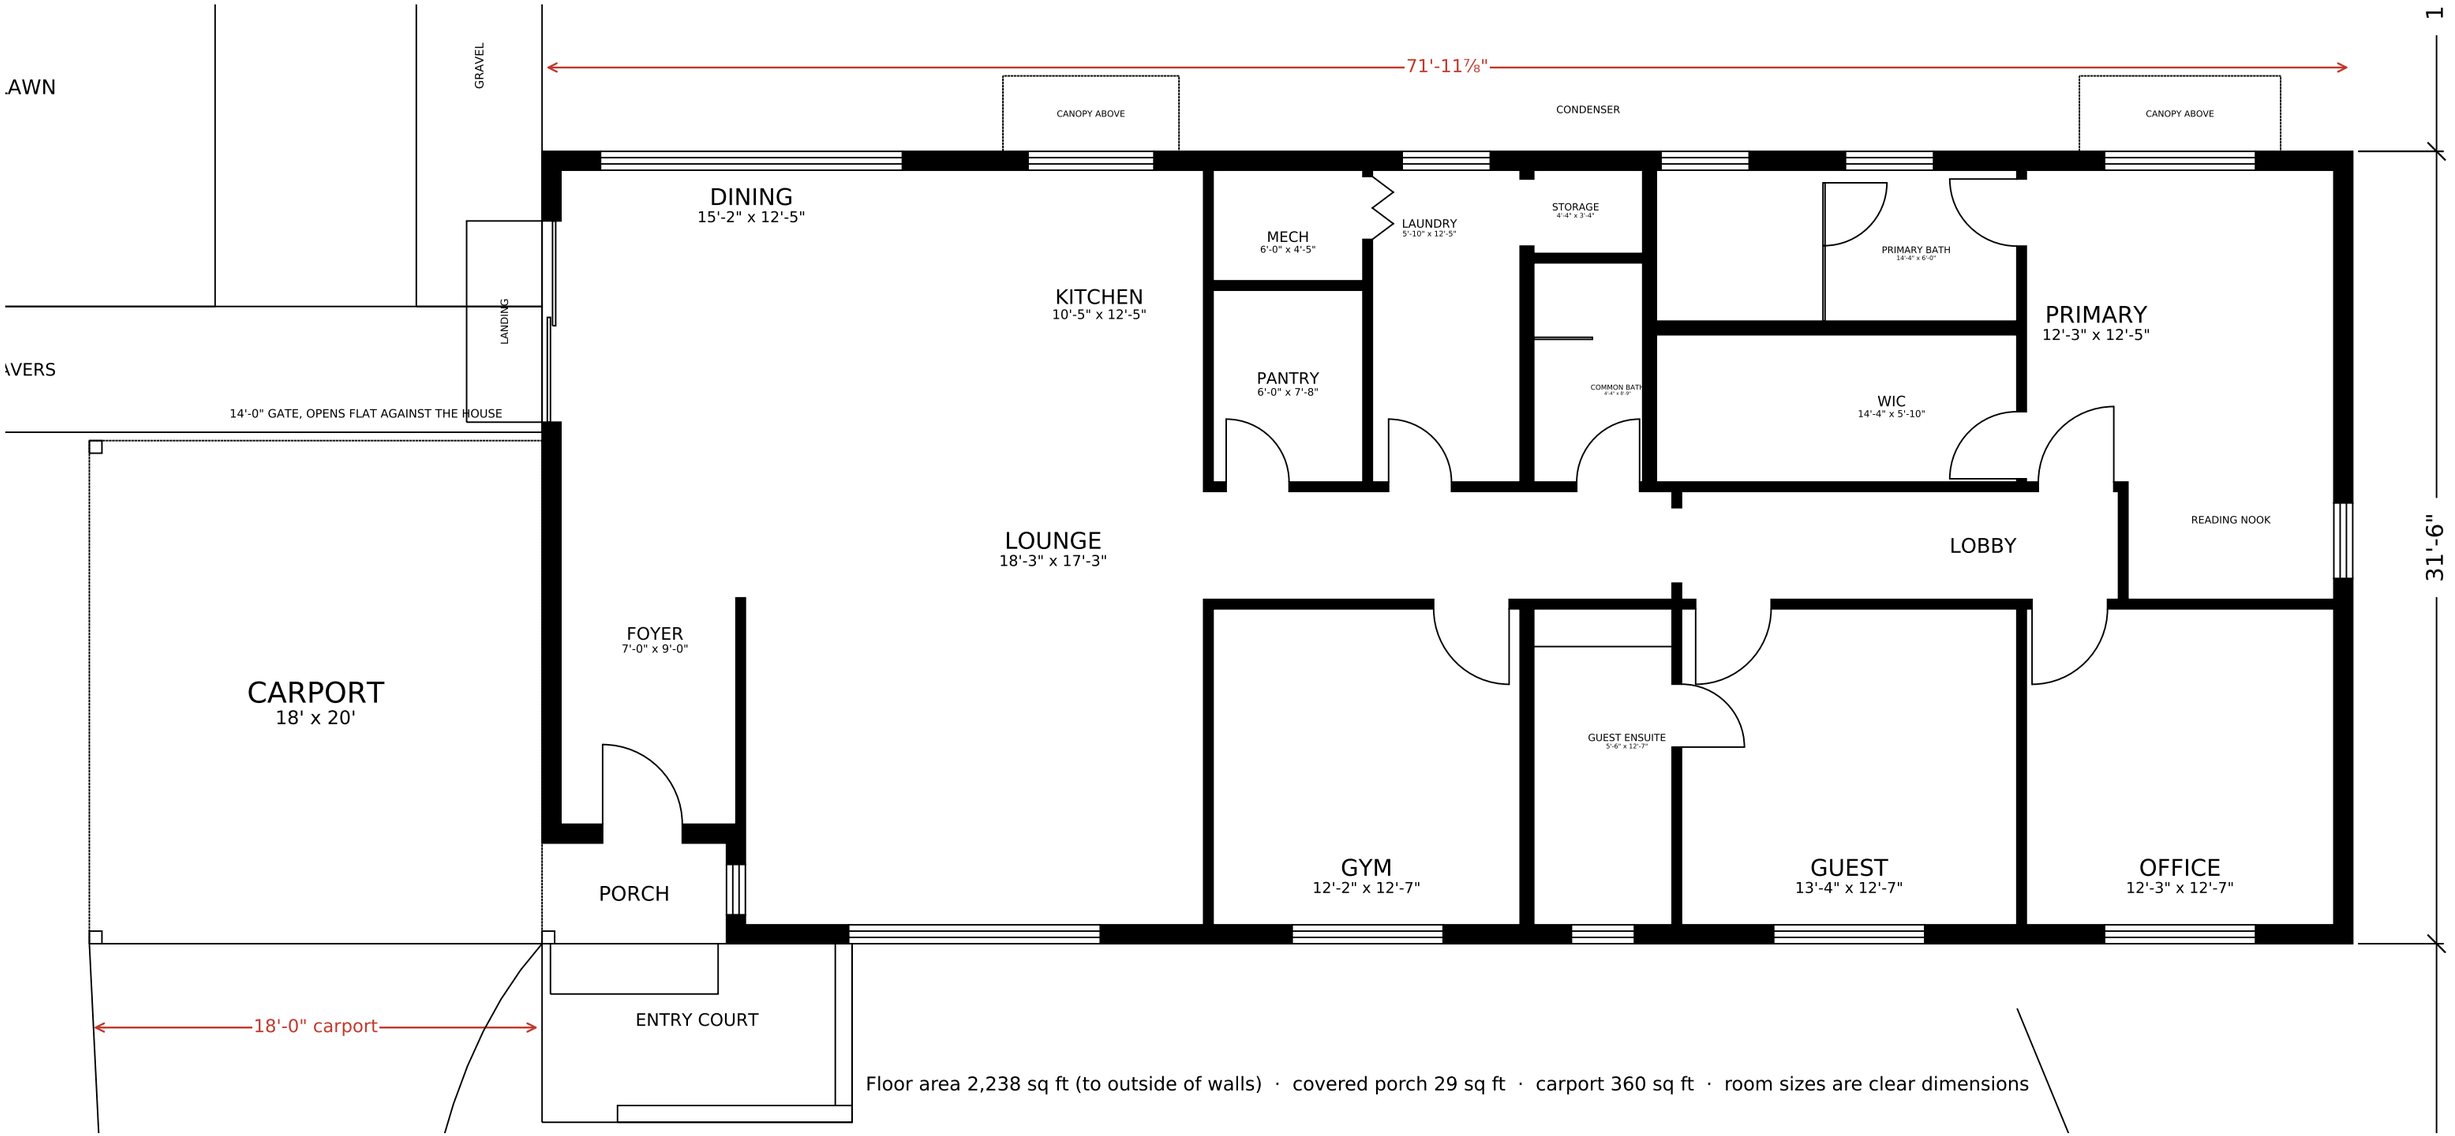


Floor area 2,238 sq ft (to outside of walls) · covered porch 29 sq ft · carport 360 sq ft · room sizes are clear dimensions

**Single-family residence rebuild (Eaton Fire), 220 Laurel Dr, Altadena CA 91001**

APN 5832-003-027 · Zone R-1, Altadena Community Standards District · Owner: Richard Acosta


PRELIMINARY ZONING CHECK SET — OWNER-PREPARED, NOT FOR CONSTRUCTION

October 15, 2026 · Dimensions in feet-inches · Plan north = street side

© 2026 Richard Acosta. All rights reserved. For 220 Laurel Dr only: not to be copied, adapted or built from anywhere else.

Floor plan & areas **Z-2**

Class A asphalt shingles · heights above finished floor · 2'-6" eaves all round (max. 2'-6" into a required yard, §22.110.090.A) · gutter along the rear edge (none on the wing's street eave)

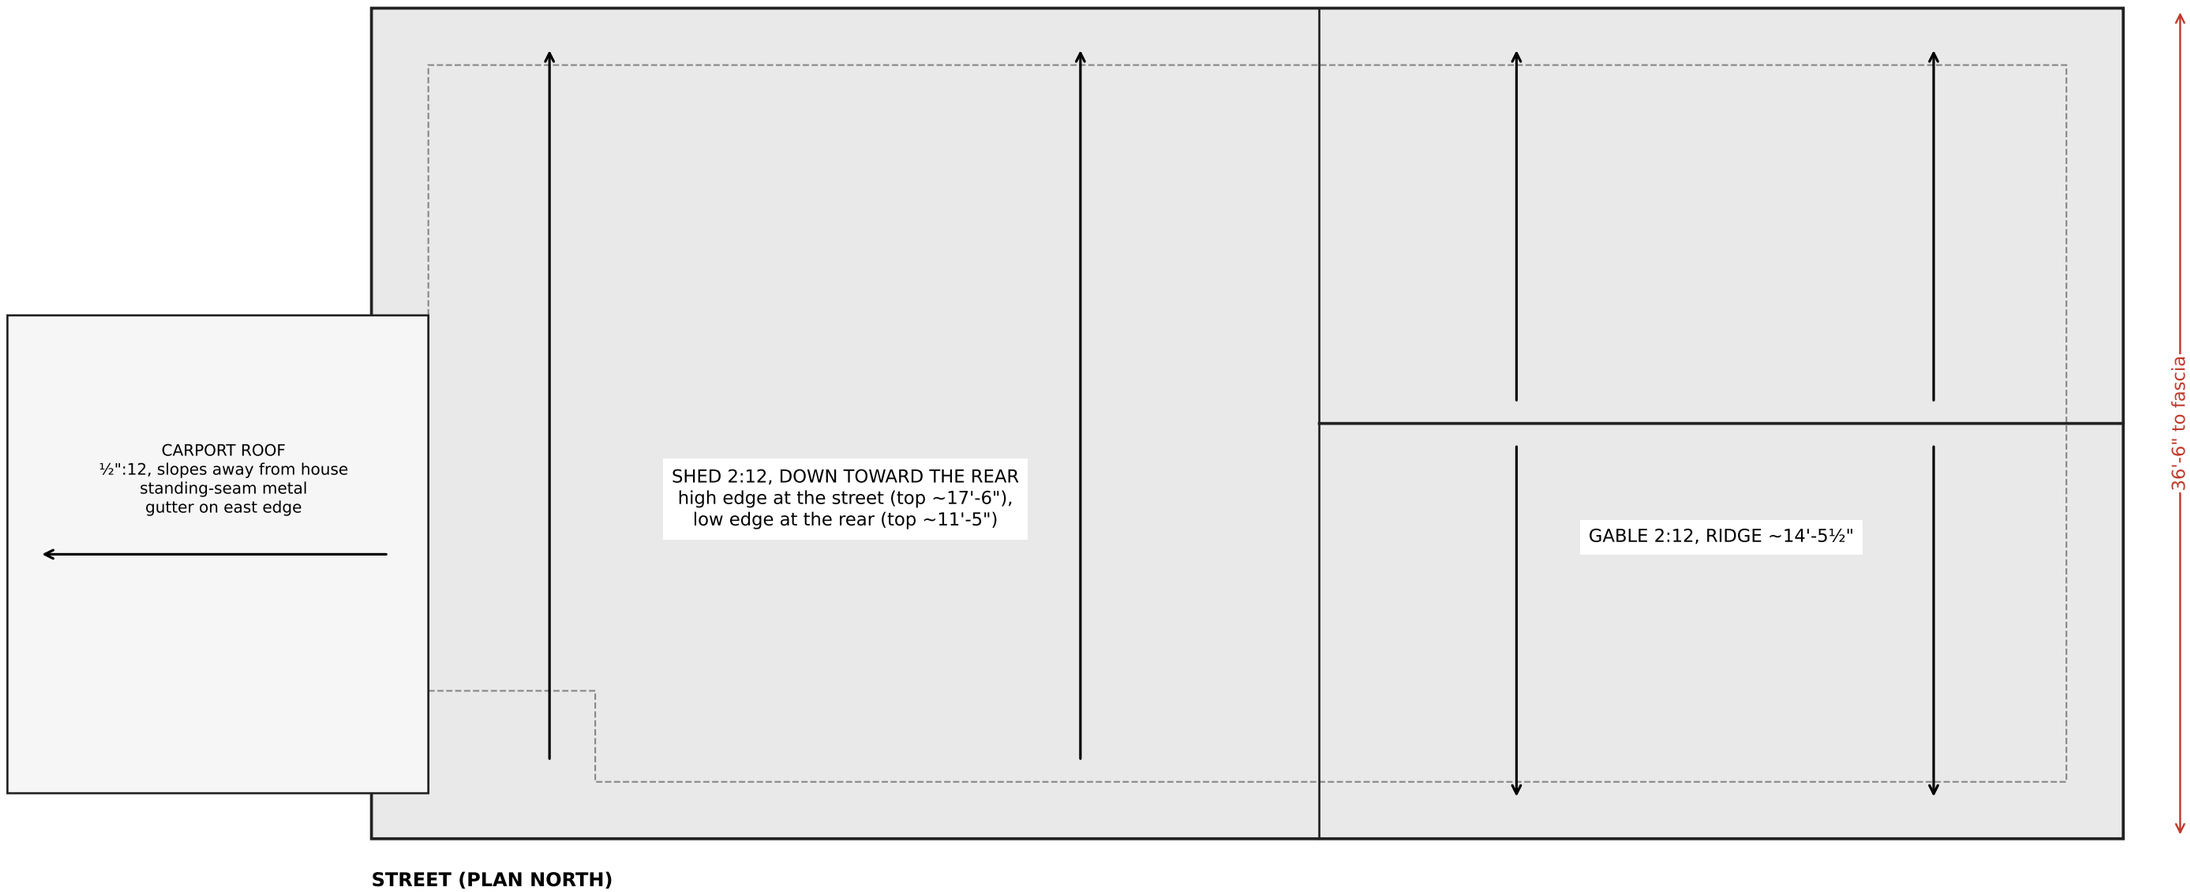


**Single-family residence rebuild (Eaton Fire), 220 Laurel Dr, Altadena CA 91001**

APN 5832-003-027 · Zone R-1, Altadena Community Standards District · Owner: Richard Acosta

PRELIMINARY ZONING CHECK SET — OWNER-PREPARED, NOT FOR CONSTRUCTION

October 15, 2026 · Dimensions in feet-inches · Plan north = street side


Roof plan **Z-3**

© 2026 Richard Acosta. All rights reserved. For 220 Laurel Dr only: not to be copied, adapted or built from anywhere else.


Heights above finished floor. The lot falls ~4' across the footprint (survey); grade lines and height above grade to follow the foundation/grading design.

Street facade articulation (§22.140.520, Table 22.140.520-C): recessed windows: all street windows set 6" behind the stucco face.
Rear: metal canopies over the kitchen and primary bedroom windows.


## NORTH (STREET) ELEVATION

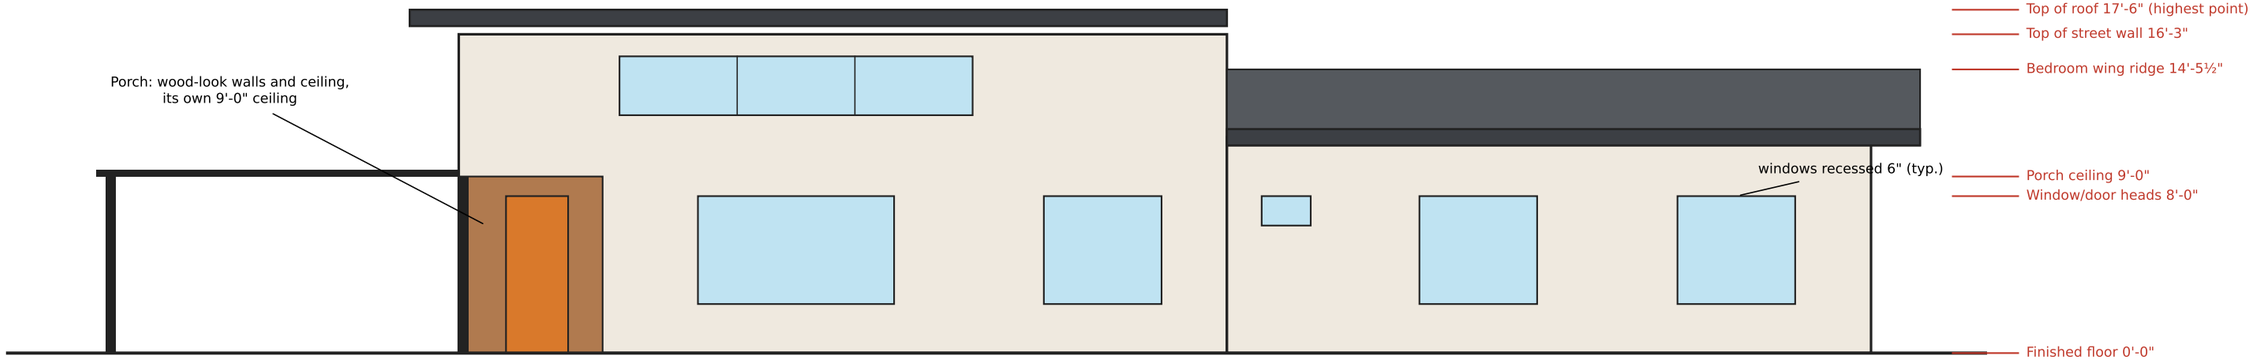



## SOUTH (REAR) ELEVATION

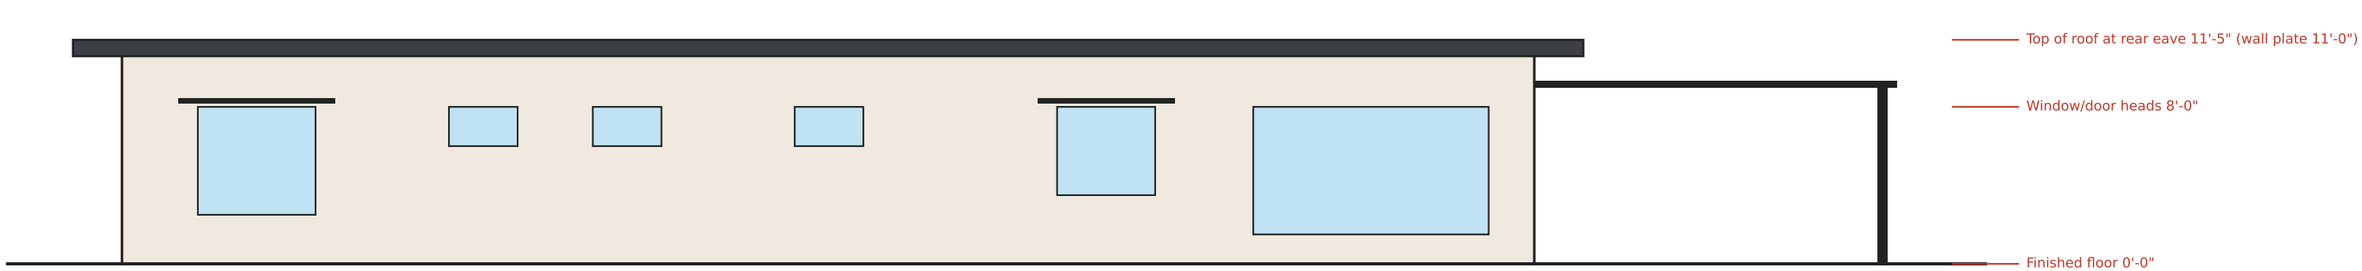


## EAST (CARPORT) ELEVATION

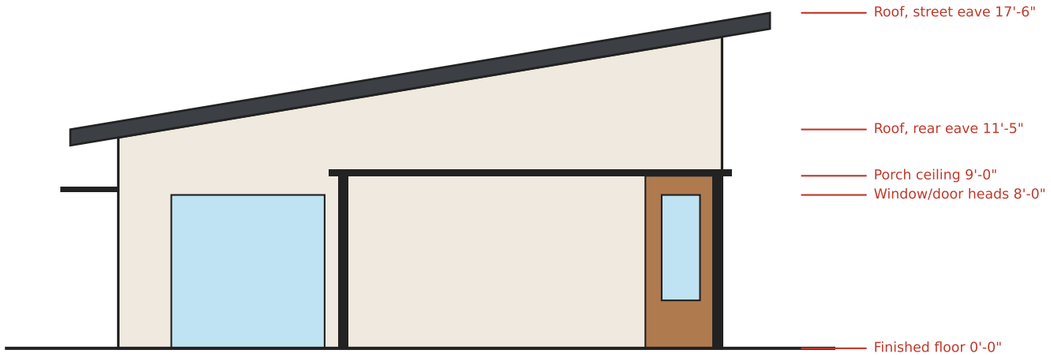


## WEST ELEVATION

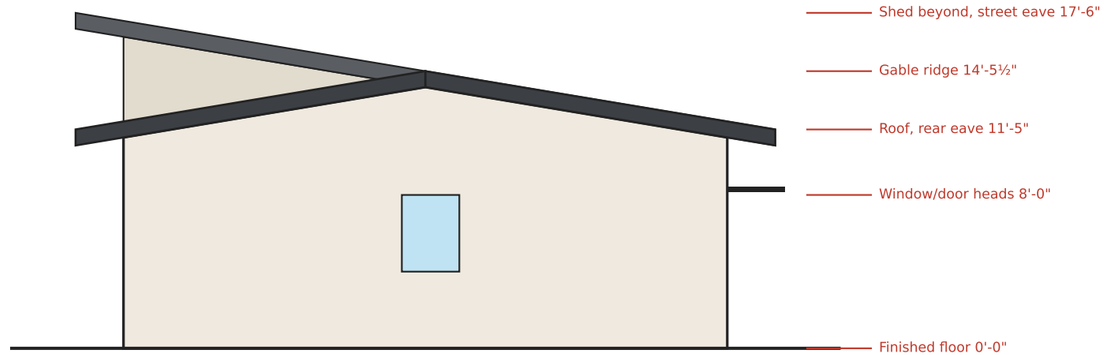


**Single-family residence rebuild (Eaton Fire), 220 Laurel Dr, Altadena CA 91001**

APN 5832-003-027 · Zone R-1, Altadena Community Standards District · Owner: Richard Acosta

PRELIMINARY ZONING CHECK SET — OWNER-PREPARED, NOT FOR CONSTRUCTION

October 15, 2026 · Dimensions in feet-inches · Plan north = street side

© 2026 Richard Acosta. All rights reserved. For 220 Laurel Dr only: not to be copied, adapted or built from anywhere else.