TOPOGRAPHIC SURVEY

220 LAUREL DRIVE, ALTADENA, CA 91001

NOTES

UNDERGROUND UTILITIES

EXCEPT FOR THOSE SHOWN HEREON NO ATTEMPT HAS BEEN MADE TO OBTAIN OR SHOW DATA CONCERNING EXISTENCE, SIZE, DEPTH, CONDITION, CAPACITY OR LOCATION OF ANY UTILITY EXISTING ON THE SITE, WHETHER PRIVATE, MUNICIPAL OR PUBLIC OWNED.

BOUNDARY & EASEMENTS

THE PROFESSIONAL SURVEYOR HAS MADE NO INVESTIGATION OR INDEPENDENT SEARCH FOR EASEMENTS OF RECORD, ENCUMBRANCES, RESTRICTIVE COVENANTS, OWNERSHIP TITLE EVIDENCE, OR ANY OTHER FACTS THAT AN ACCURATE AND CURRENT TITLE SEARCH MAY DISCLOSE.

NOT ALL TREES ARE SHOWN HEREON.

THIS IS NOT A BOUNDARY SURVEY.

LEGEND AND SYMBOLS ABBREVIATIONS

	LOT LINE	AC	: ASPHALTIC CONCRETE
	CENTER LINE	CB	: CATCH BASIN
	CHAIN LINK FENCE	CONC	: CONCRETE
	IRON FENCE	CL	: CENTER LINE
	WOODEN FENCE	CD	: CURB DRAIN
	BLOCK WALL	AD	: AREA DRAIN
	RETAINING WALL	W	: WATER
	STREET LIGHT	FDC	: FIRE DEPARTMENT CONNECTION
	TREE	HB	: HOSE BIB
	PINE TREE	EG	: EDGE OF GUTTER
	PALM TREE	ICV	: IRRIGATION CONTROL VALVE
PP	POWER POLE	FH	: FIRE HYDRANT
STREET	STREET SIGN	FF	: FINISH FLOOR
STLT	STREET LIGHT POOL BOX	FL	: FLOW LINE
WM	WATER METER	FS	: FINISH SURFACE
	WATER VALVE	FW	: FACE OF WALL
	FIRE HYDRANT	TC	: TOP OF CURB
BLD	BOLLARD	TRW	: TOP OF RETAINING WALL
GM	GAS METER	TW	: TOP OF WALL
	GUY WIRE	BFL	: BACK FLOW PREVENTER
ELT	ELECTRICAL BOX	C/O	: CLEANOUT
PARK	PARKING SIGN	SS	: SANITARY SEWER
		FW	: FRONT OF WALK
		BW	: BACK OF WALK
		LE	: LANDSCAPE EDGE

BRIEF LEGAL DESCRIPTION

PORTION OF LOT 11 OF JOHNSTON AND HAY TRACT , IN THE UNINCORPORATED TERRITORY, COUNTY OF LOS ANGELES, STATE OF CALIFORNIA, AS PER MAP RECORDED IN BOOK 9, PAGE 50 OF MAPS, IN THE OFFICE OF THE COUNTY RECORDER OF SAID COUNTY.

BASIS OF BEARING

THE BEARINGS SHOWN HEREON ARE BASED ON THE BEA RING S67°36'30"E OF A COURSE IN THE STREET CENTERLINE OF LAUREL DRIVE AS SHOWN ON THE MAP OF JOHNSTON AND HAY TRACT, M.B. 9, PAGE 50.


BENCHMARK

ASSUMED BENCHMARK:

FND. SPK ELEVATION = 1437.46 FT.

DATE OF SURVEY

SEPTEMBER 9, 2026

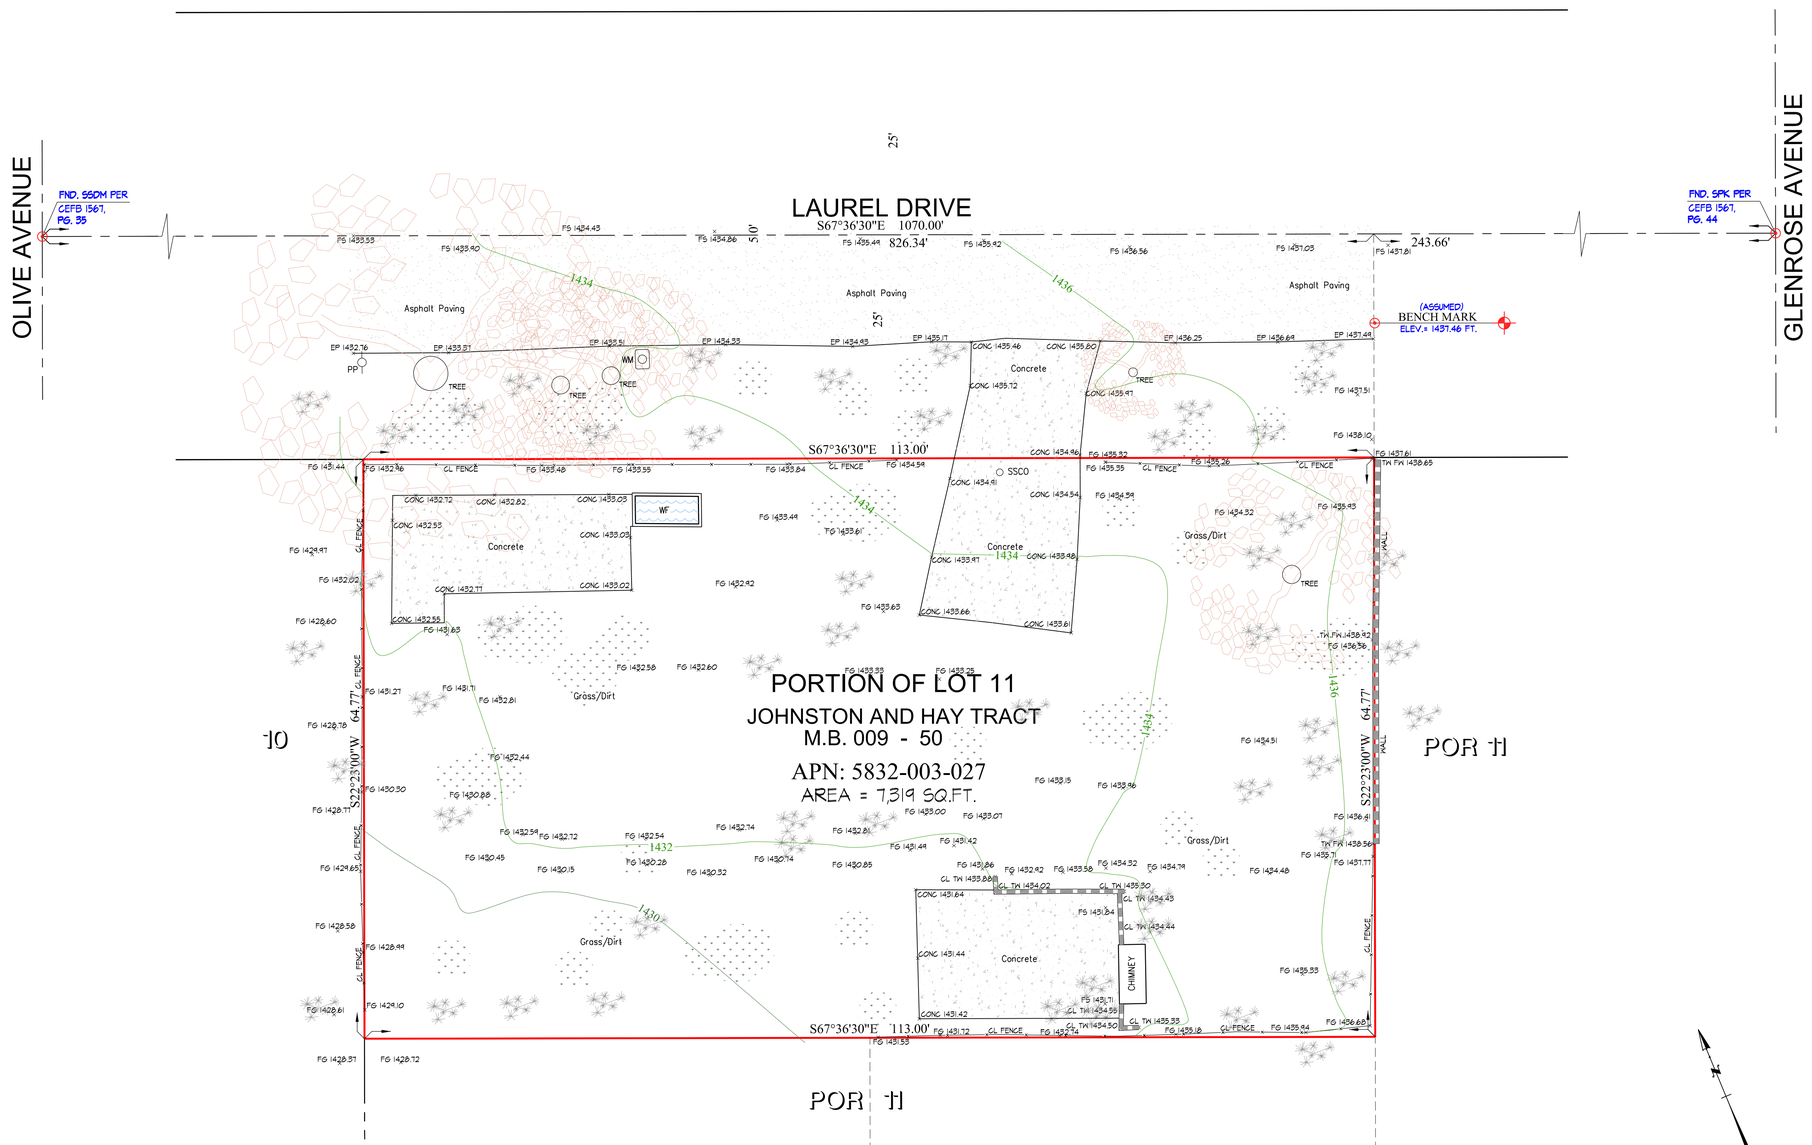

PLAN
SCALE: 1" = 8'

8' 4' 0' 8' 16'
GRAPHIC SCALE

PROFESSIONAL LAND SURVEYOR
GEORGE BARAJAS No. 8399
STATE OF CALIFORNIA

GEORGE BARAJAS, PLS 8399 — 09-10-2026 DATE