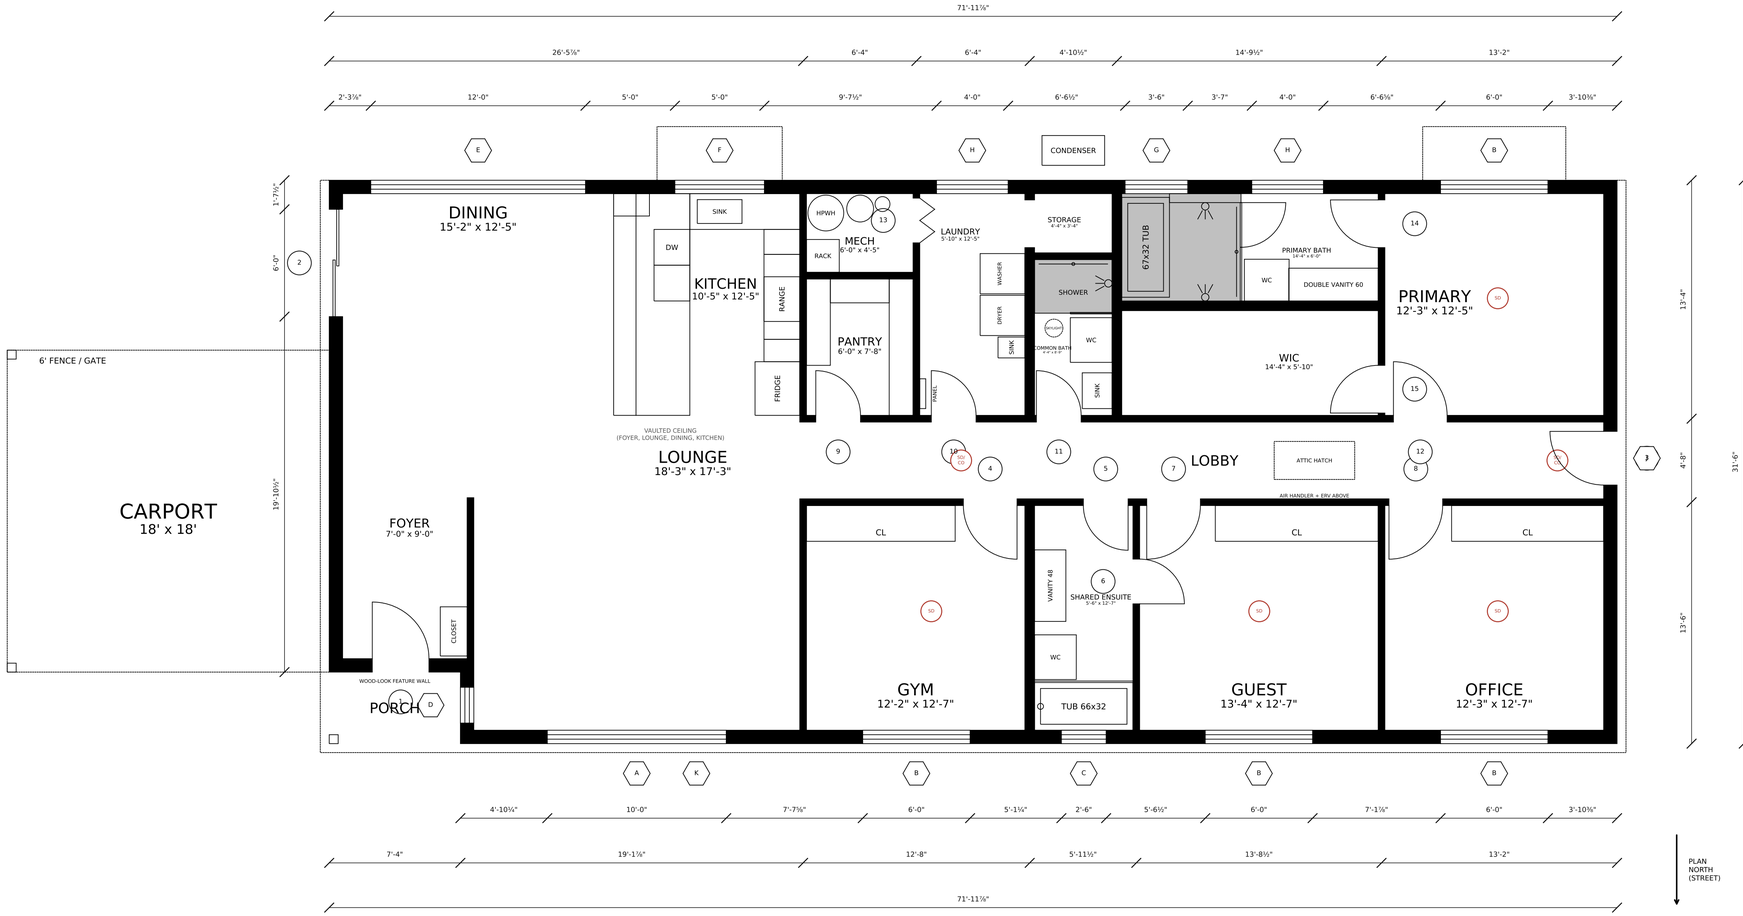


FLOOR PLAN 1/4" = 1'-0"

GENERAL NOTES

1. Dimensions are to wall centrelines; exterior walls to the outside face of framing + finish (9" walls).
2. Walls: exterior 2x6 with 1" rigid insulation and stucco; interior 2x4; plumbing walls 2x6.
3. Ceilings 9'-0" unless noted. The foyer, lounge, dining and kitchen are vaulted under the roof (see sections).
4. Doors 8'-0" high unless noted. Exterior doors and glazing per CRC R337 (VHFHSZ).
5. All exterior glazing dual-pane with at least one tempered pane (CRC R337.8.2.1). Fully tempered where noted (CRC R308.4).
6. Bedroom windows meet emergency escape: 5.7 sq ft net clear, 20" min width, 24" min height, sill 44" max (CRC R310).
7. Smoke alarms in each bedroom and outside the sleeping areas, hard-wired, interconnected, battery backup (CRC R314). Combination smoke / CO alarms outside the sleeping areas (CRC R315).
8. All-electric: heat pump HVAC (air handler and ERV in the sealed attic; outdoor unit at the rear wall), heat pump water heater (HPWH) in the mechanical closet.
9. Fire sprinklers throughout (NFPA 13D); plans by the sprinkler designer (deferred submittal).
10. Attic access: 22" x 54" pull-down ladder in the hall, 30" min headroom above (CRC R807.1).
11. Furniture not shown; closets, cabinets and fixtures shown for reference.

DOOR SCHEDULE

TAG	LOCATION	SIZE (W x H)	TYPE	NOTES
1	PORCH / FOYER (exterior)	3'-2" x 8'-0"	Hinged	Solid core 1-3/8"+ or noncombustible (CRC R337.8.3); weatherstripped
2	DINING (exterior)	6'-0" x 8'-0"	Sliding glass door	Solid core 1-3/8"+ or noncombustible (CRC R337.8.3); weatherstripped; dual-pane tempered glazing
3	LOBBY (exterior)	3'-0" x 7'-0"	Hinged, half-lite	Solid core 1-3/8"+ or noncombustible (CRC R337.8.3); weatherstripped; dual-pane tempered glazing; 3'-0" x 1'-6" transom above (window J)
4	GYM / LOBBY	3'-0" x 8'-0"	Hinged	
5	SHARED ENSUITE / LOBBY	2'-6" x 8'-0"	Hinged	privacy lock
6	SHARED ENSUITE / GUEST	2'-6" x 8'-0"	Hinged	privacy lock
7	GUEST / LOBBY	3'-0" x 8'-0"	Hinged	
8	OFFICE / LOBBY	3'-0" x 8'-0"	Hinged	
9	LOUNGE / PANTRY	2'-6" x 8'-0"	Hinged	
10	LOUNGE / LAUNDRY	2'-6" x 8'-0"	Hinged	solid core (noise)
11	LOBBY / COMMON BATH	2'-6" x 8'-0"	Hinged	privacy lock; solid core (noise)
12	LOBBY / PRIMARY	3'-0" x 8'-0"	Hinged	
13	MECH / LAUNDRY	2'-6" x 8'-0"	Bifold, louvered	solid core (noise); louvered for the water heater's air
14	PRIMARY BATH / PRIMARY	2'-8" x 8'-0"	Hinged	privacy lock
15	WIC / PRIMARY	2'-8" x 8'-0"	Hinged	

WINDOW SCHEDULE

TAG	QTY	LOCATION	SIZE (W x H)	SILL	OPERATION	NOTES
A	1	Lounge	10'-0" x 5'-6"	2'-6"	Fixed center, slider each end	
B	4	Gym, Guest, Office, Primary	6'-0" x 5'-6"	2'-6"	Horizontal slider	Emergency escape (egress)
C	1	Shared Ensuite	2'-6" x 1'-6"	6'-6"	Awning	Tempered: at tub / wet room, obscure
D	1	Foyer	2'-0" x 5'-6"	2'-6"	Fixed, reeded glass	Tempered: beside the front door
E	1	Dining	12'-0" x 6'-6"	1'-6"	Fixed, two units mulled	Tempered: large pane, low sill
F	1	Kitchen	5'-0" x 4'-6"	3'-6"	Horizontal slider	Over the sink
G	1	Primary Bath	3'-6" x 2'-0"	6'-0"	Awning	Tempered: at tub / wet room
H	2	Laundry, Primary Bath	4'-0" x 2'-0"	6'-0"	Awning	High window
J	1	Lobby	3'-0" x 1'-6"	7'-2"	Fixed transom	Tempered: above the door
K	1	Lounge	18'-2⅛" x 3'-0"	12'-1½"	Fixed (mulled units)	Clerestory over the lounge

LEGEND

- (1) Door tag (see door schedule)
- (A) Window tag (see window schedule)
- (SD) Smoke alarm (SD), smoke / CO alarm (SD/CO)
- Overhead: band, canopy, attic hatch, skylight

ACOSTA RESIDENCE

Single-family residence
fire rebuild (Eaton Fire)

220 Laurel Dr
Altadena, CA 91001
APN 5832-003-027

Zone R-1 · Altadena CSD
Very High Fire Hazard Severity Zone

Owner: Richard Acosta

Prepared by: _____

Structural: by engineer (separate sheets)

DRAFT FOR REVIEW not for construction

Date: October 15, 2026
Revisions:

© 2026 Richard Acosta. All rights reserved. These drawings are for 220 Laurel Dr only. Not to be copied, adapted, sold or built from on any other site.

FLOOR PLAN, DOOR & WINDOW SCHEDULES

A-2