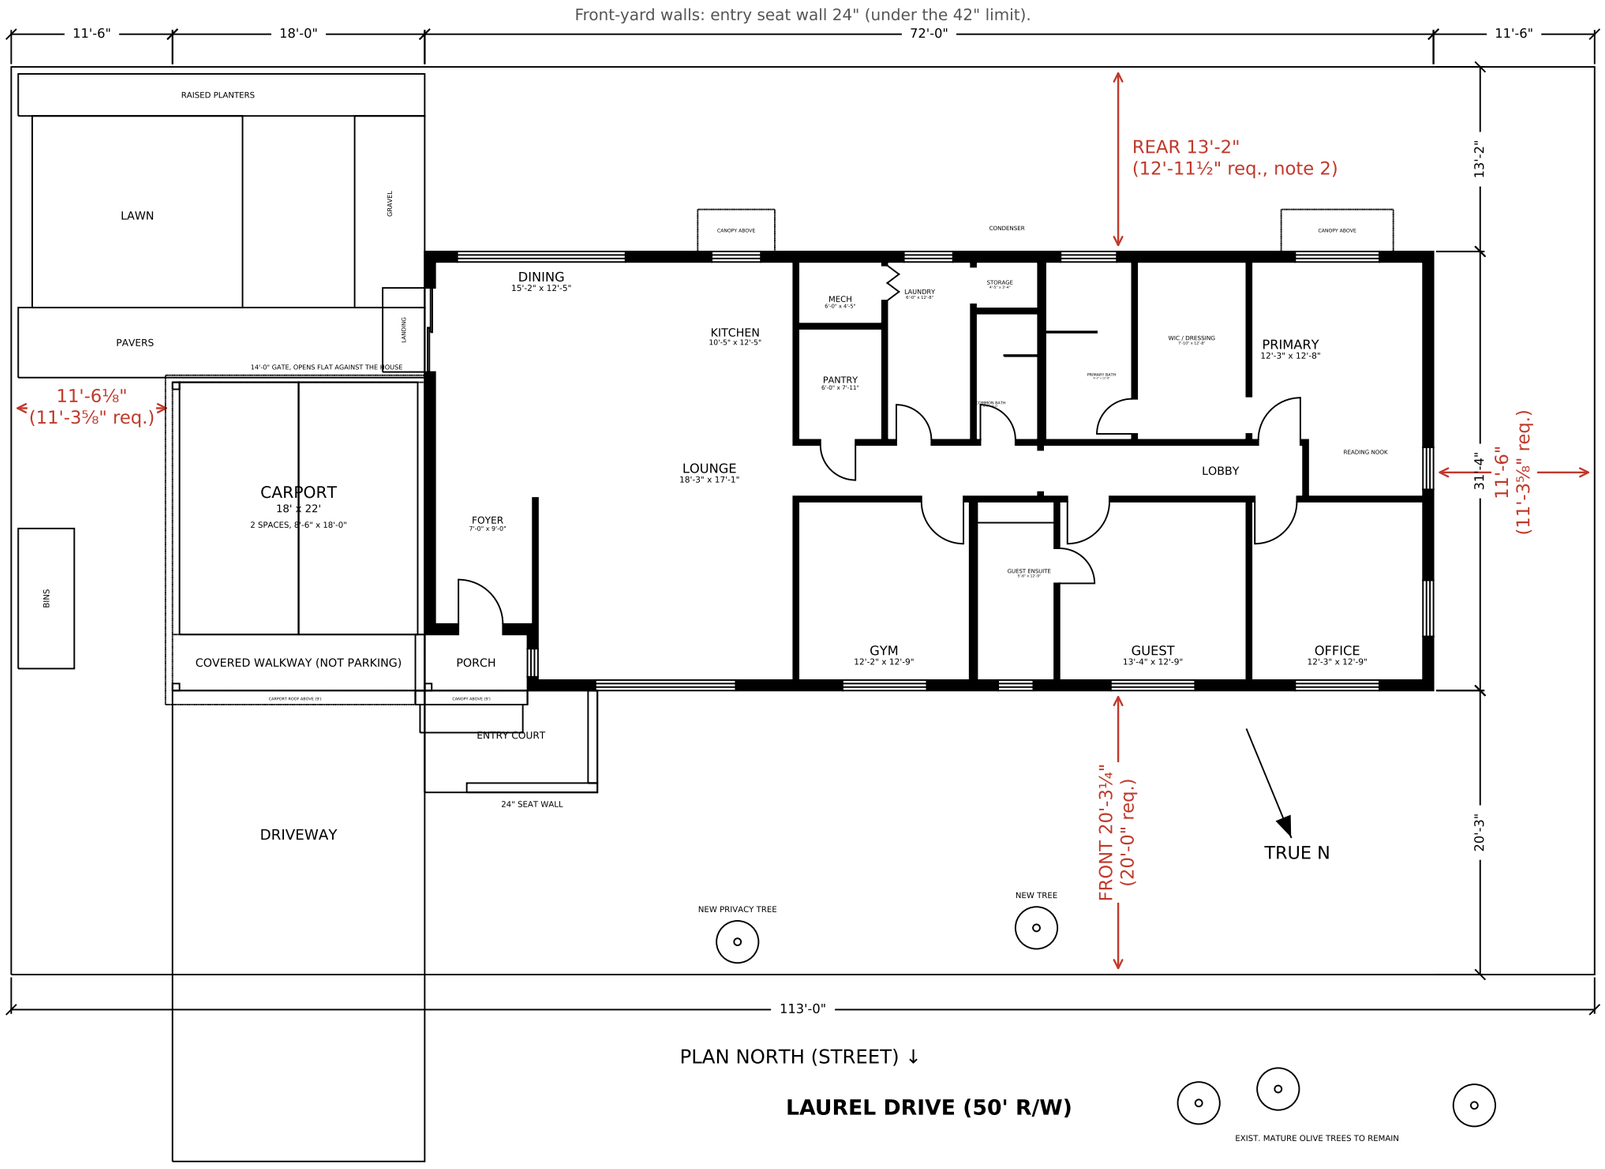


PROJECT DATA

Scope	Non-like-for-like rebuild, 1-story SFR + attached carport (Eaton Fire)
Zone / overlay	R-1 · Altadena CSD · VHFHSZ
Lot	113.00' x 64.77' = 7,319 sq ft
Floor area (to outside of walls)	2,226 sq ft
Covered porch	37 sq ft
Carport (attached, open)	396 sq ft
Lot coverage	2,660 sq ft (36.3%)
CSD limit (¼ lot + 1,000)	2,830 sq ft (coverage and floor area)
Stories / max height	1 story · ~17'-5⅝" above finished floor (top of roof at the street eave)
Bedrooms / baths	4 / 3
Parking	2 covered, 8'-6" x 18'-0" each, behind the front door; the carport's front 4'-0" is a covered walkway, not parking (8' x 5' covered porch)

SETBACKS	required · provided
Front (street)	20'-0" · 20'-3¼"
Rear (§22.110.080.D)	12'-11½" · 13'-2"
Side, west	11'-3⅝" · 11'-6"
Side, east (carport)	11'-3⅝" · 11'-6⅛"

Glazing (Title 24 check)	~427 sq ft (~19.2% of floor)

NOTES
1. Setbacks measured to the finished outside face of exterior walls (stucco; eaves excluded).
2. Side setback taken as 10% of lot width. Rear yard on a shallow lot (§22.110.080.D): the lot is 64.77' deep (under 75'), so the rear yard is 20% of the average depth, 12'-11½" (confirmed with Planning).
3. Heights are above finished floor; the lot falls ~4' across the footprint, so height above grade depends on the foundation design (to be set with the civil).
4. Lot lines, lot dimensions and existing trees are from the owner's topographic survey (available on request).
5. Eaves 2'-6", the rear 2'-0": the projection is measured to its farthest point, gutter included (Planning); within 2'-6" into each required yard (§22.110.090.A), more than 2'-6" from every lot line, no supports in the yards.
6. Rear window canopies 3'-0" deep (§22.110.090.B: up to 5' into the rear yard): over the windows only, 1' past each side, no supports in the yard.
7. Covered entry porch 8'-0" x 5'-0" (Table 22.140.520-D), 1'-0" into the front yard under a 9' canopy (§22.110.090.D.2 allows 5'); parking sits behind the front door.

Single-family residence rebuild (Eaton Fire), 220 Laurel Dr, Altadena CA 91001


APN 5832-003-027 · Zone R-1, Altadena Community Standards District · Owner: Richard Acosta

PRELIMINARY ZONING CHECK SET — OWNER-PREPARED, NOT FOR CONSTRUCTION

October 15, 2026 · Dimensions in feet-inches · Plan north = street side

Site plan & project data **Z-1**

© 2026 Richard Acosta. All rights reserved. For 220 Laurel Dr only: not to be copied, adapted or built from anywhere else.

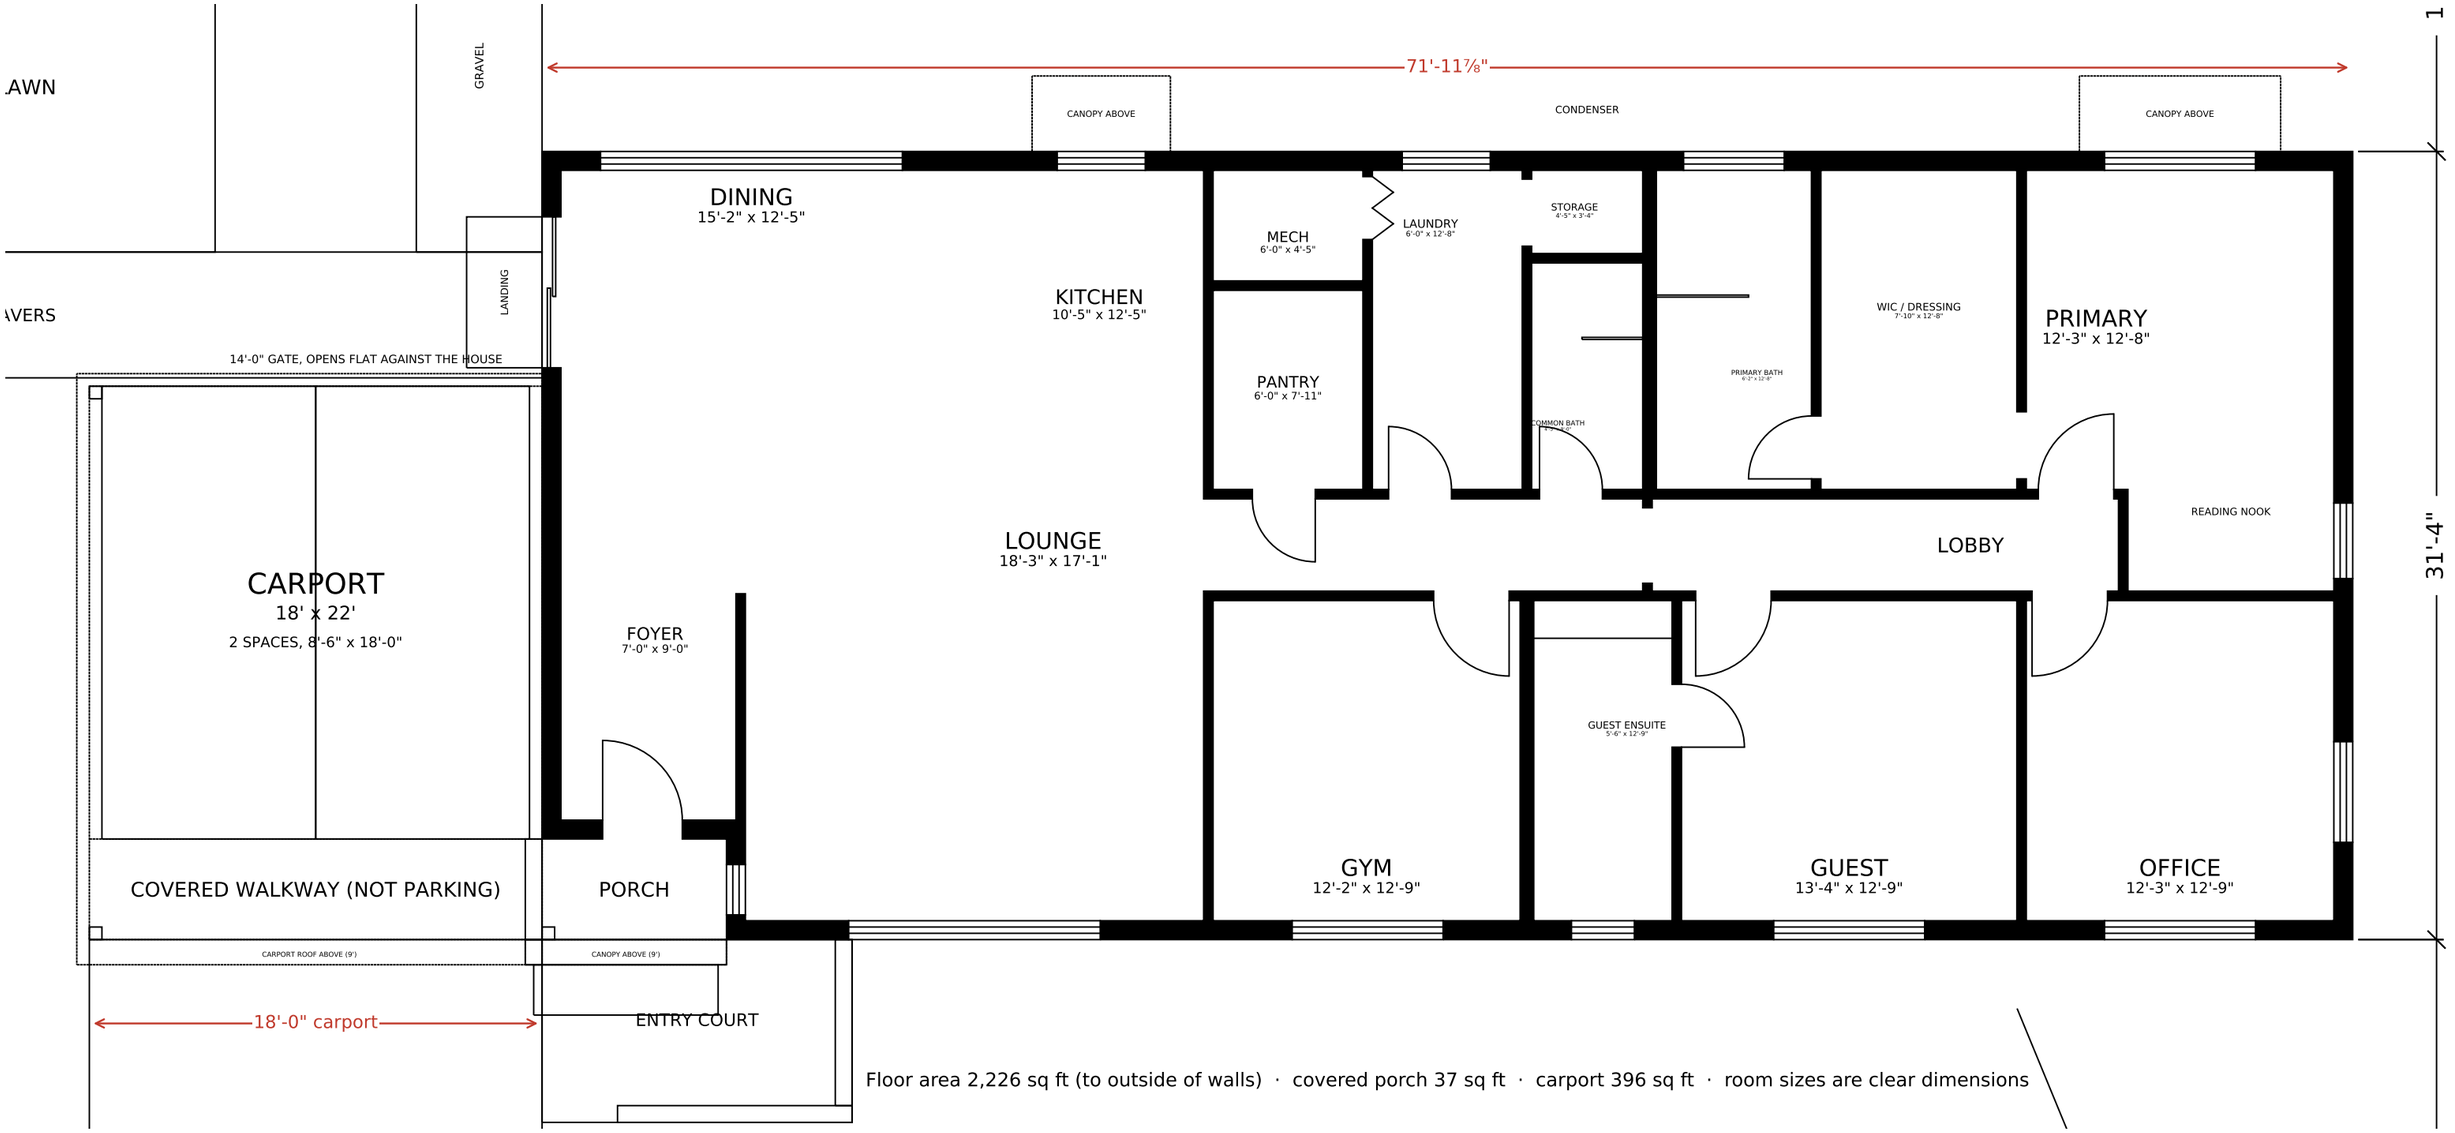

Floor area 2,226 sq ft (to outside of walls) · covered porch 37 sq ft · carport 396 sq ft · room sizes are clear dimensions

Single-family residence rebuild (Eaton Fire), 220 Laurel Dr, Altadena CA 91001

APN 5832-003-027 · Zone R-1, Altadena Community Standards District · Owner: Richard Acosta


PRELIMINARY ZONING CHECK SET — OWNER-PREPARED, NOT FOR CONSTRUCTION

October 15, 2026 · Dimensions in feet-inches · Plan north = street side

© 2026 Richard Acosta. All rights reserved. For 220 Laurel Dr only: not to be copied, adapted or built from anywhere else.

Floor plan & areas **Z-2**

Class A asphalt shingles · heights above finished floor · 2'-6" eaves, 2'-0" at the rear (max. 2'-6" into a required yard, gutter included) · gutter along the rear edge (none on the wing's street eave)

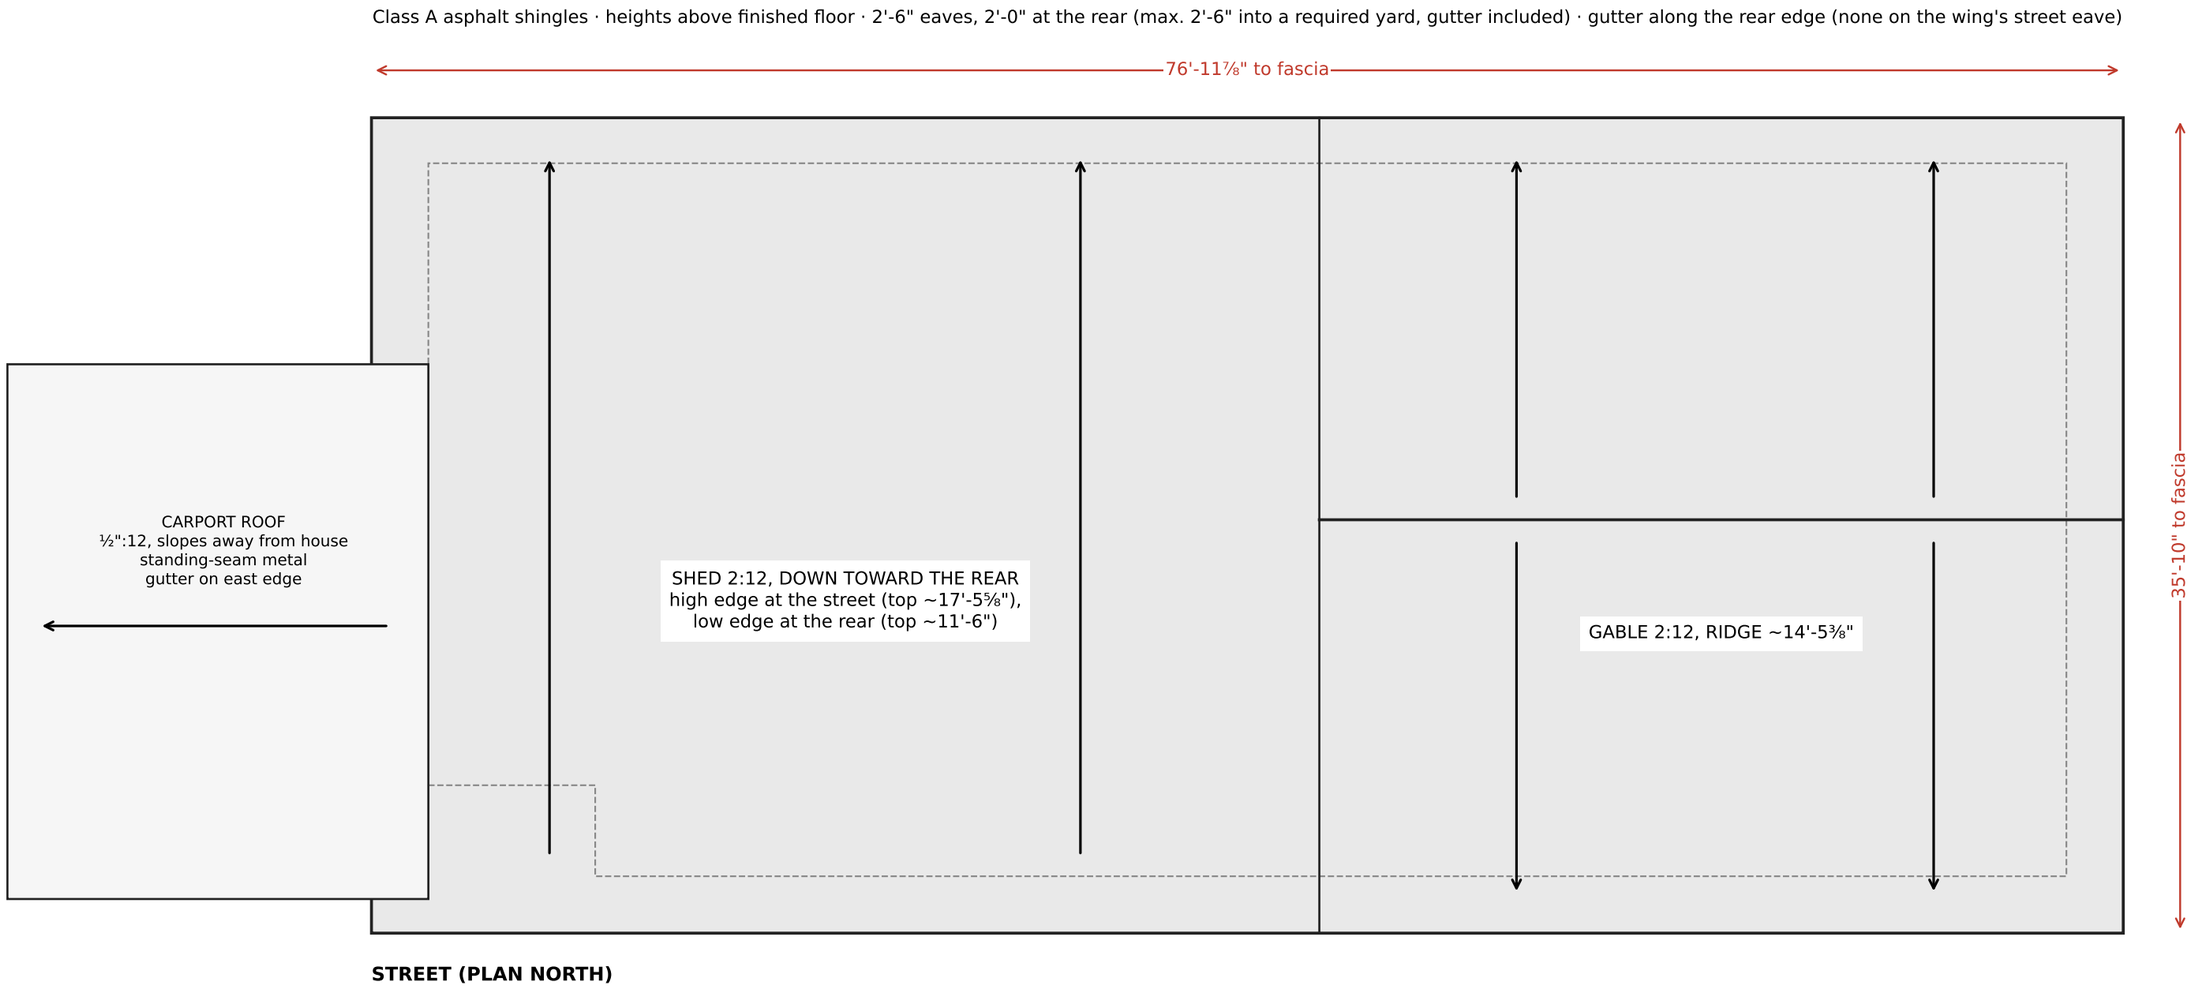

Single-family residence rebuild (Eaton Fire), 220 Laurel Dr, Altadena CA 91001

APN 5832-003-027 · Zone R-1, Altadena Community Standards District · Owner: Richard Acosta

PRELIMINARY ZONING CHECK SET — OWNER-PREPARED, NOT FOR CONSTRUCTION

October 15, 2026 · Dimensions in feet-inches · Plan north = street side


© 2026 Richard Acosta. All rights reserved. For 220 Laurel Dr only: not to be copied, adapted or built from anywhere else.

Roof plan **Z-3**

Heights above finished floor. The lot falls ~4' across the footprint (survey); grade lines and height above grade to follow the foundation/grading design.


Street facade articulation (§22.140.520, Table 22.140.520-C): recessed windows: the punched street windows (~158 sq ft) set 6" behind the stucco face, ~74% of the facade's window area (~212 sq ft; the clerestory band is flush); the standard asks for over 50%.
Rear: metal canopies over the kitchen and primary bedroom windows.

NORTH (STREET) ELEVATION

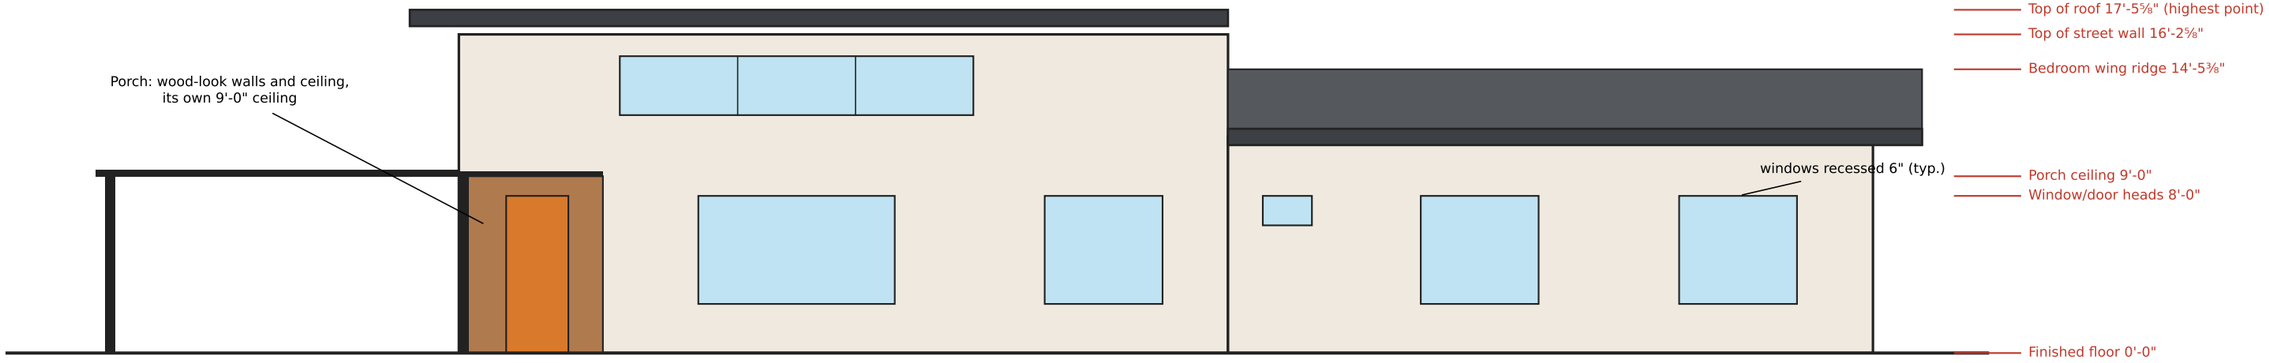


SOUTH (REAR) ELEVATION

EAST (CARPORT) ELEVATION

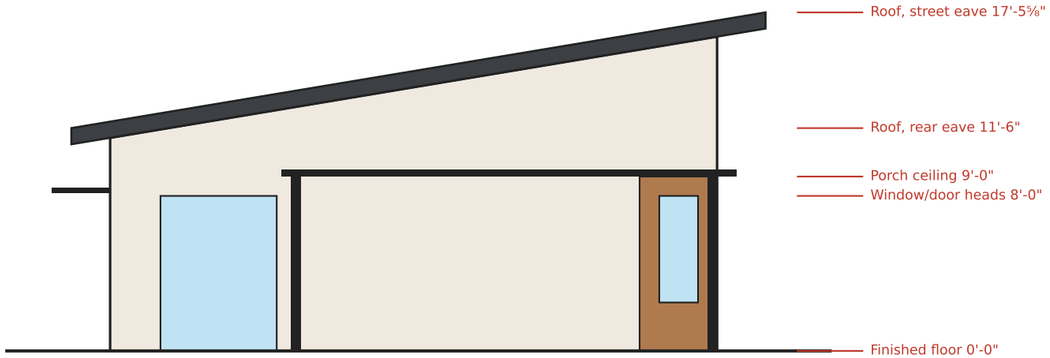

WEST ELEVATION

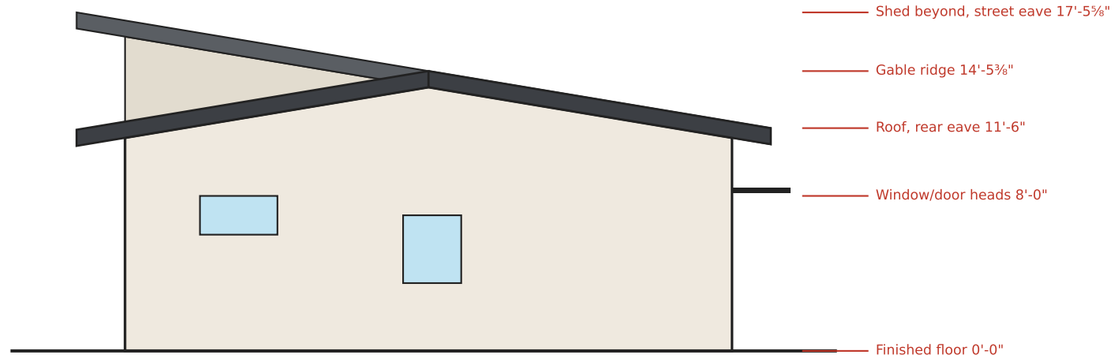

Single-family residence rebuild (Eaton Fire), 220 Laurel Dr, Altadena CA 91001

APN 5832-003-027 · Zone R-1, Altadena Community Standards District · Owner: Richard Acosta

PRELIMINARY ZONING CHECK SET — OWNER-PREPARED, NOT FOR CONSTRUCTION

October 15, 2026 · Dimensions in feet-inches · Plan north = street side

© 2026 Richard Acosta. All rights reserved. For 220 Laurel Dr only: not to be copied, adapted or built from anywhere else.