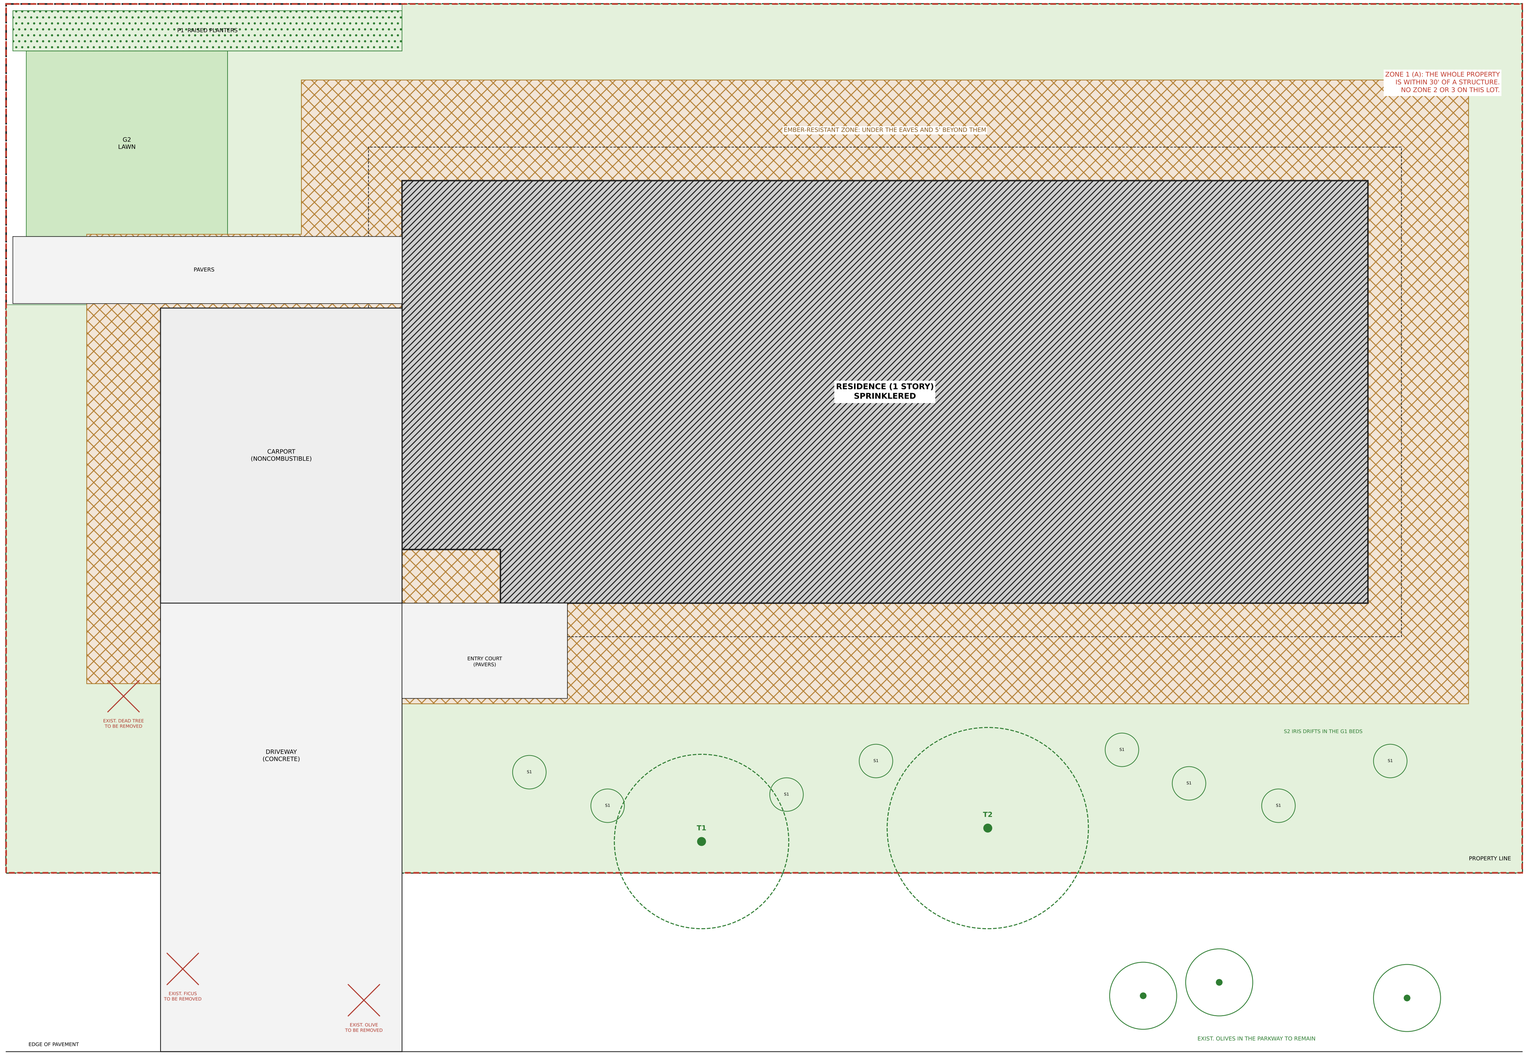


LAUREL DRIVE

FUEL MODIFICATION PLAN 3/16" = 1'-0" (PLAN NORTH = STREET)

Ember-resistant zone: noncombustible surfaces
G1 ground cover (irrigated)
G2 lawn (irrigated, mowed)
Zone 1 (A) limit, 30'
Eaves / roof edge
Tree, mature canopy

Prepared by the owner, Richard Acosta. Drawn to scale from the owner's topographic survey and site plan. Fuel Modification Unit: forestryfuelmodification@fire.lacounty.gov, (626) 969-5205.

PLANT LEGEND (all Zone 1 / A)

Key	Botanical name	Common name	County zone / min. distance	Size at maturity	Qty	Size	Notes
T1	Heteromeles arbutifolia	Toyon	A / 15'	10'-15' h x 10'-15' w	1	15 gal	Privacy tree, tree form; canopy clear of the roof
T2	Cercis occidentalis	Western redbud	A / 10'	10'-18' h x 10'-15' w	1	15 gal	Deciduous; canopy clear of the roof
S1	Salvia greggii	Autumn sage	A / 10'	2'-3' h x 3' w	8	5 gal	Accents only, 10'+ from the house, widely spaced
S2	Iris douglasiana	Pacific coast iris	A	1'-2' h x 2' w	12	1 gal	Front beds
G1	Dymondia margaretae / Achillea tomentosa	Dymondia / woolly yarrow	A	under 6" h	per area	flats @ 12" o.c.	Front, side and rear ground cover
G2	Festuca arundinacea (dwarf) with Trifolium repens	Tall fescue lawn with microclover	A	mowed, 3"-4"	per area	sod / seed	Courtyard lawn, irrigated and mowed
P1	Heuchera spp. / Cyrtomium falcatum	Coral bells / holly fern	A	1'-2' h	per area	1 gal	Raised planters along the rear fence

EXISTING VEGETATION

Botanical name	Common name	Location	Disposition
Olea europaea (3)	Olive, mature	Public parkway, outside the property	Existing to remain
Unidentified	Lot tree (dead)	On the lot, beside the carport	Remove
Olea europaea	Olive	Public parkway, in the driveway	Remove (County permit)
Ficus sp.	Ficus	Public parkway, ~13'-6" east of the olive	Remove (County permit)

FUEL MODIFICATION NOTES (LA County Fire, Fuel Modification Plan Notes)
EMBER-RESISTANT ZONE (shown hatched)
1. Extends 5' beyond the edge of any combustible structure, appendage or projection, measured from the eaves and the porch canopy; includes the areas beneath eaves. Kept free of materials and plants receptive to embers: concrete, pavers, gravel or decomposed granite only; no organic mulch, plants, wood furniture or storage.

ZONE 1 (A), 0-30' (the whole property)
2. Irrigated to keep vegetation healthy and fire resistant.
3. Primarily mowed lawn, low ground covers and widely spaced low shrubs; no woody plants over 12" within 10' of the house, none in front of windows.
4. Trees: dwarf or under 25' tall and wide at maturity, canopies never over a roof (T1, T2). No large shrubs beneath tree canopies.
5. No vines on any structure. No hedges over 6' within 10' of the house.
6. Species per the County Fuel Modification Plant List; scientific names shown in the legend.

EXISTING VEGETATION
7. The burned lot is cleared: no existing on-lot vegetation remains except as shown. The dead lot tree beside the carport is removed; the olive and ficus in the east parkway are removed under a County permit. The parkway olives are outside the property and remain.

IRRIGATION
8. Automatic system with a weather-based controller: drip at trees, shrubs and ground cover; spray at the lawn. Maintained year-round.

MAINTENANCE
9. Keep roofs, eaves and gutters free of leaves and debris; keep the ember-resistant zone free of anything ember-receptive.
10. Remove dead or dying plants, plant litter and dead wood in all zones; prune to break up horizontal and vertical fuel ladders; remove invasive species; keep the irrigation working.
11. Compliance is a year-round responsibility; inspections may occur at any time. All future planting per the County Fuel Modification Guidelines, approved before installation.

Approval of this plan covers only the codes reviewed by the Fuel Modification Unit; it does not replace any other agency's approval.

ACOSTA RESIDENCE

Single-family residence
fire rebuild (Eaton Fire)

220 Laurel Dr
Altadena, CA 91001
APN 5832-003-027

Zone R-1 · Altadena CSD
Very High Fire Hazard Severity Zone

Owner: Richard Acosta

Prepared by: _____

Structural: by engineer (separate sheets)

DRAFT FOR REVIEW
not for construction

Date: October 15, 2026
Revisions:

© 2026 Richard Acosta. All rights reserved. These drawings are for 220 Laurel Dr only. Not to be copied, adapted, sold or built from on any other site.

FUEL MODIFICATION PLAN

FM-1