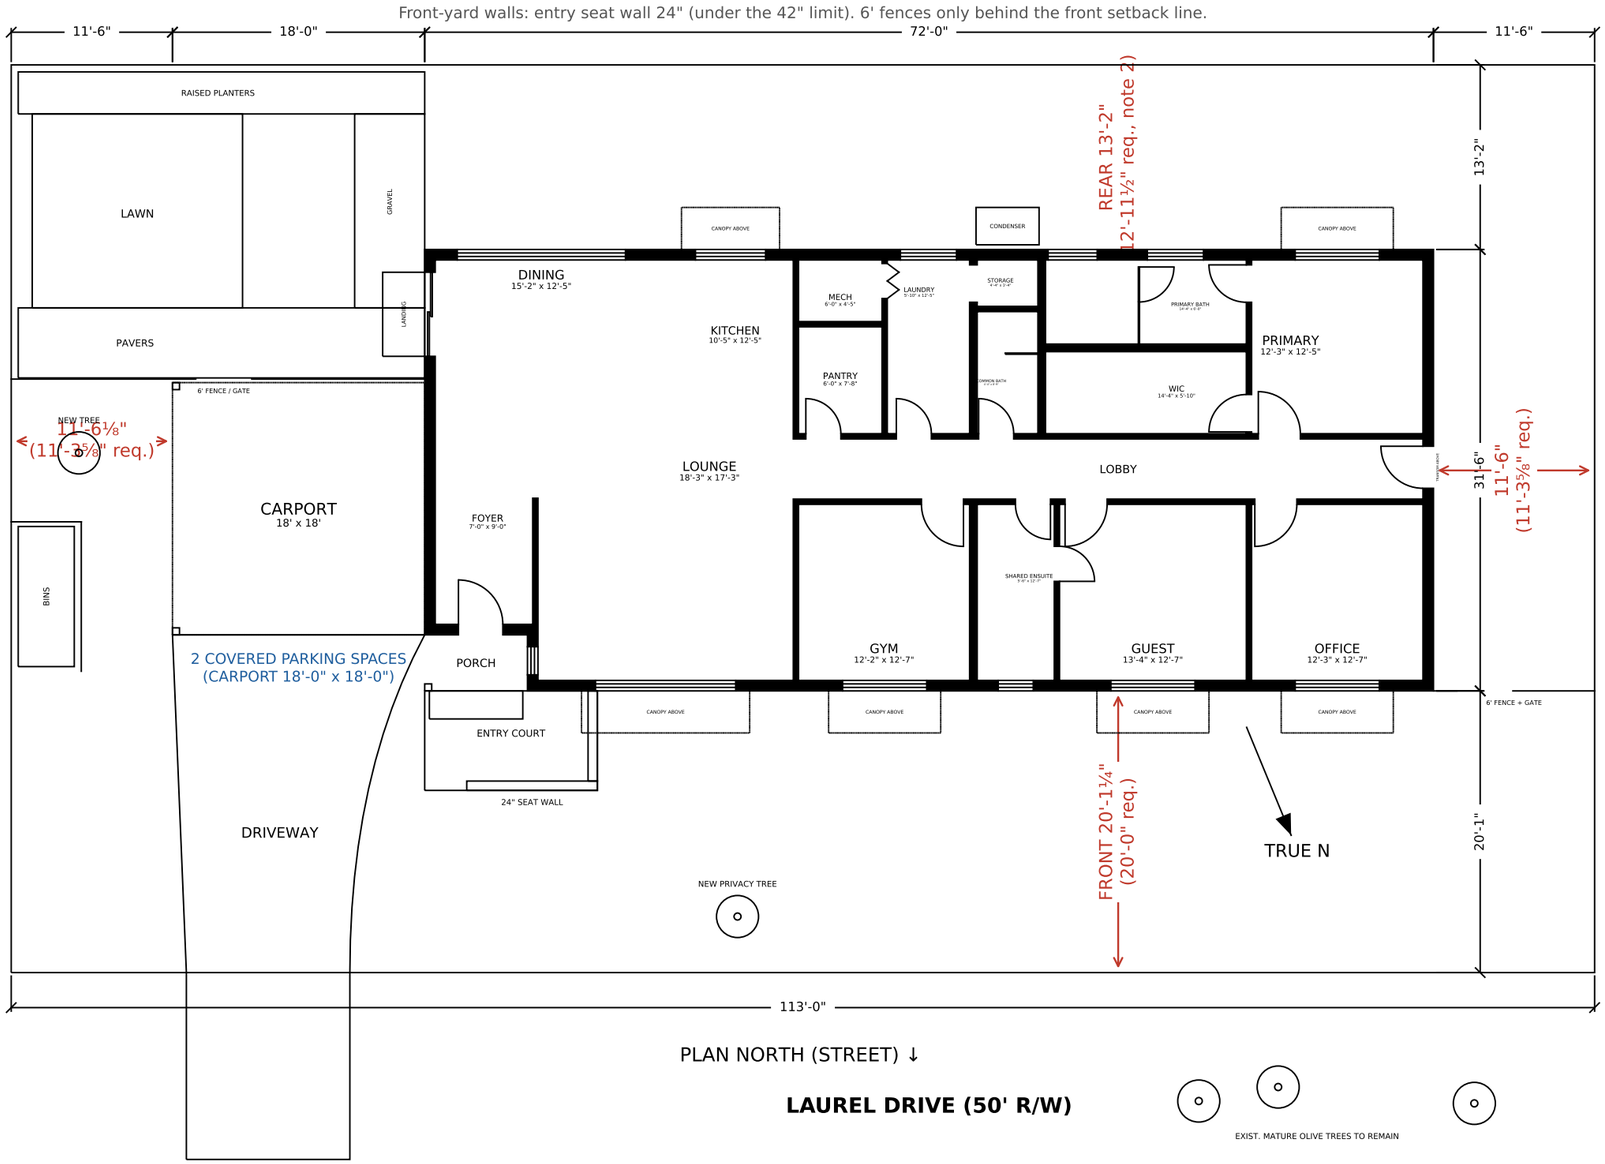


PROJECT DATA

Scope	Non-like-for-like rebuild, 1-story SFR + attached carport (Eaton Fire)
Zone / overlay	R-1 · Altadena CSD · VHFHSZ
Lot	113.00' x 64.77' = 7,319 sq ft
Floor area (to outside of walls)	2,238 sq ft
Covered porch	29 sq ft
Carport (attached, open)	324 sq ft
Lot coverage	2,592 sq ft (35.4%)
CSD limit (¼ lot + 1,000)	2,830 sq ft (coverage and floor area)
Stories / max height	1 story · ~17'-6" above finished floor (top of roof at the street eave)
Bedrooms / baths	4 / 3
Parking	2 covered (carport)

SETBACKS	required · provided
Front (street)	20'-0" · 20'-1¼"
Rear (§22.110.080.D)	12'-11½" · 13'-2"
Side, west	11'-3⅝" · 11'-6"
Side, east (carport)	11'-3⅝" · 11'-6⅛"

Glazing (Title 24 check)	~432 sq ft (~19.3% of floor)

NOTES
1. Setbacks measured to the outside face of exterior walls (eaves excluded).
2. Side setback taken as 10% of lot width. Rear yard on a shallow lot (§22.110.080.D): the lot is 64.77' deep (under 75'), so the rear yard is 20% of the average depth, 12'-11½". Please confirm it applies under the Altadena CSD.
3. Heights are above finished floor; the lot falls ~4' across the footprint, so height above grade depends on the foundation design (to be set with the civil).
4. Existing retaining wall and chimney (survey) to be removed.
5. Survey: topographic survey on file (APN above).
6. Eaves 2'-6" all round: the most an eave may project into a required yard (§22.110.090.A); more than 2'-6" from every lot line, no supports in the yards.
7. Window canopies 3'-0" deep, street and rear (§22.110.090.B: up to 5' into front and rear yards): over the windows only, 1' past each side, no supports in the yards.


Single-family residence rebuild (Eaton Fire), 220 Laurel Dr, Altadena CA 91001

APN 5832-003-027 · Zone R-1, Altadena Community Standards District · Owner: Richard Acosta

PRELIMINARY ZONING CHECK SET — OWNER-PREPARED, NOT FOR CONSTRUCTION

October 15, 2026 · Dimensions in feet-inches · Plan north = street side

Site plan & project data **Z-1**

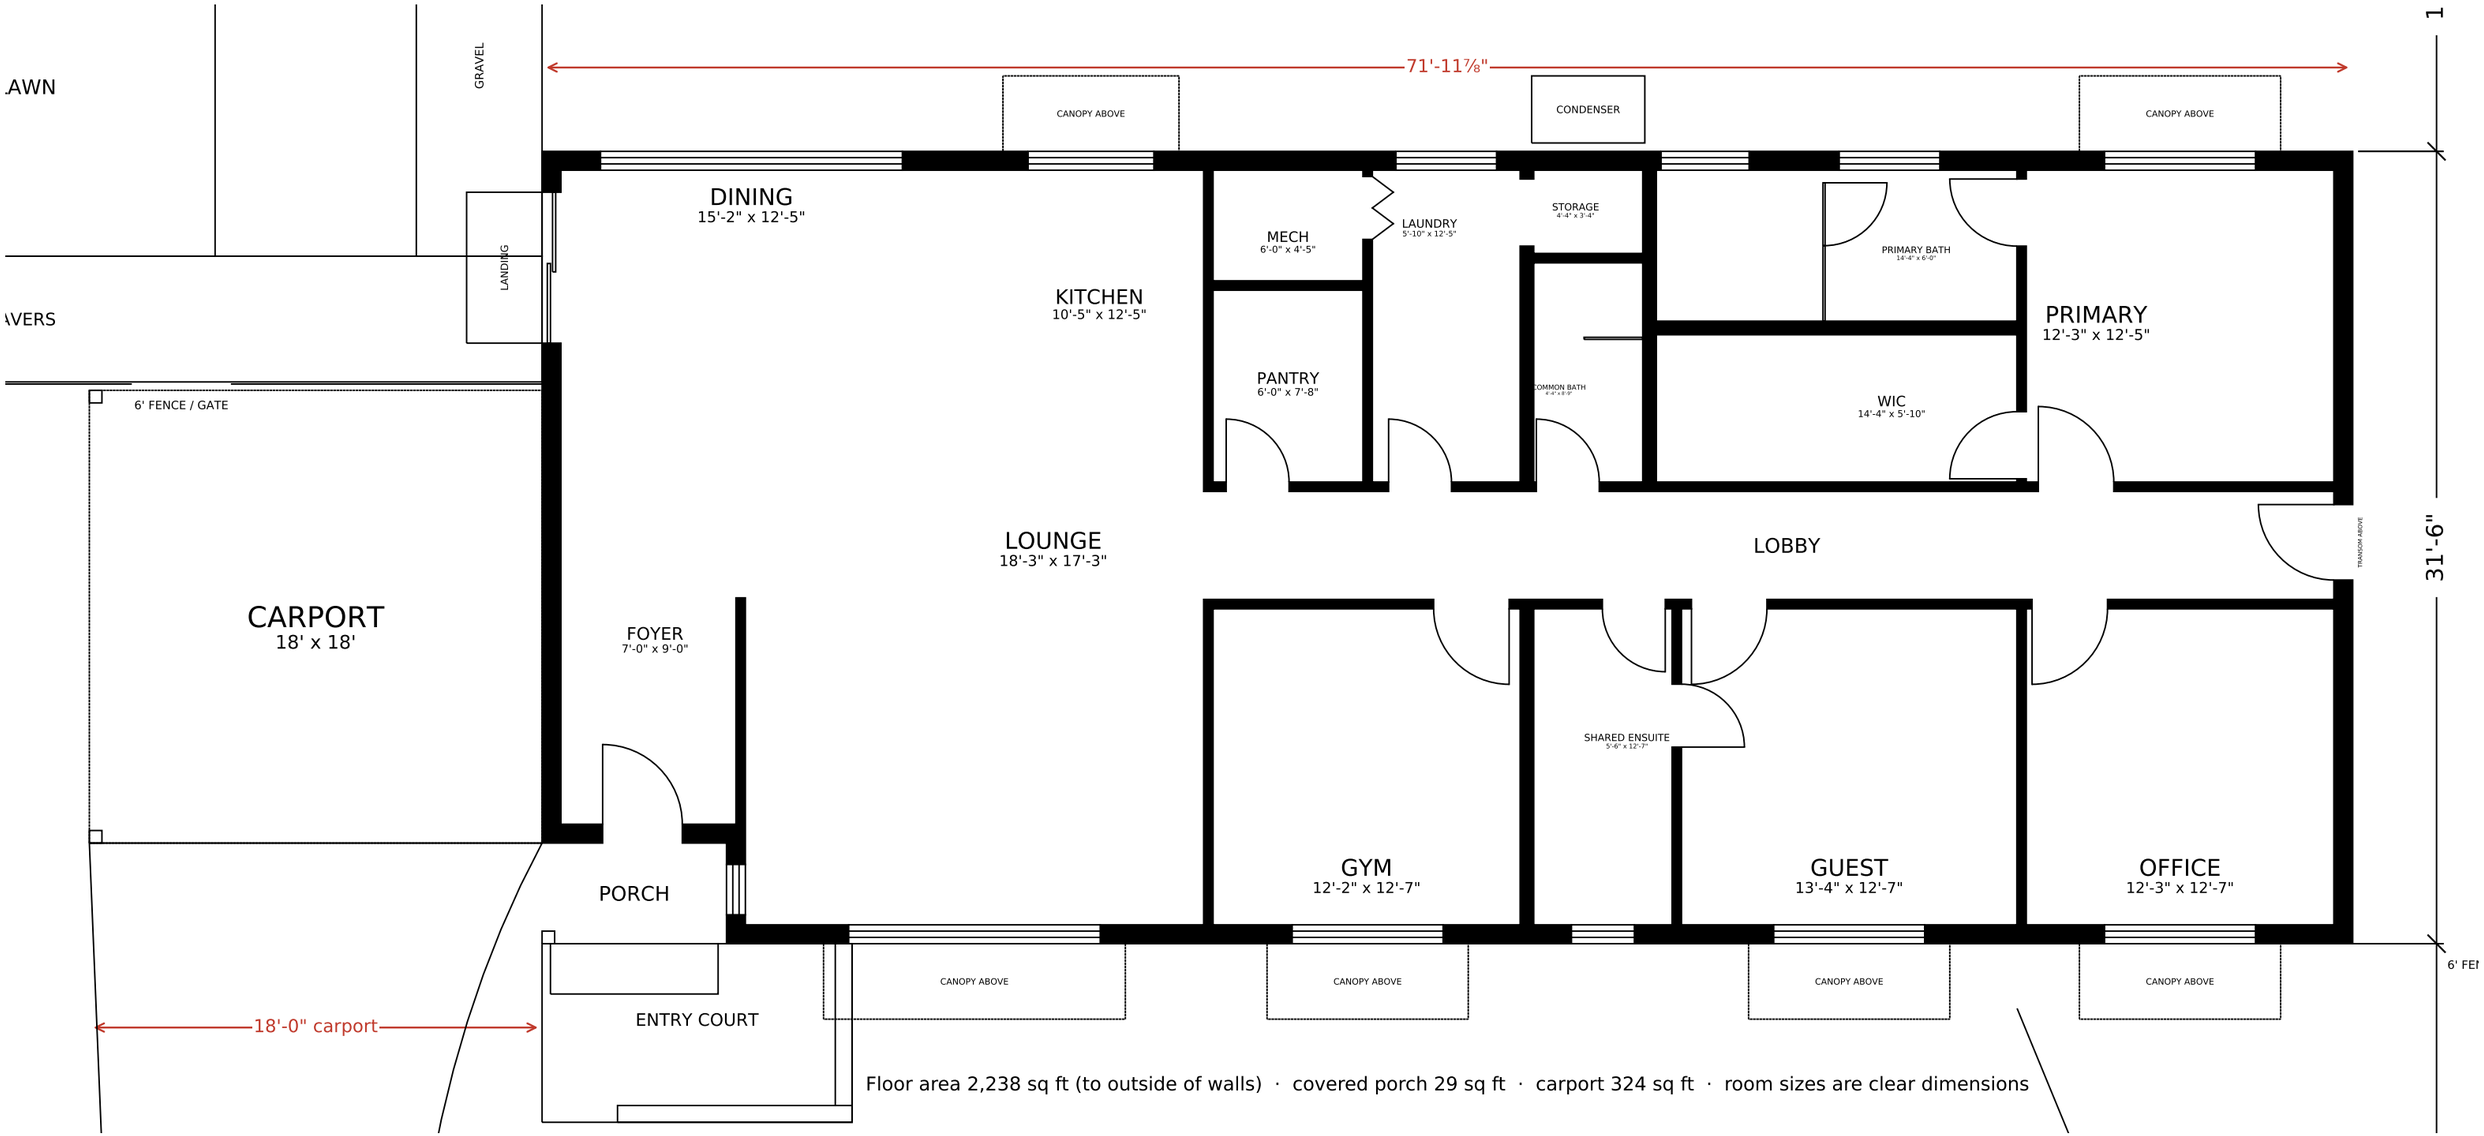

Floor area 2,238 sq ft (to outside of walls) · covered porch 29 sq ft · carport 324 sq ft · room sizes are clear dimensions


Single-family residence rebuild (Eaton Fire), 220 Laurel Dr, Altadena CA 91001

APN 5832-003-027 · Zone R-1, Altadena Community Standards District · Owner: Richard Acosta

PRELIMINARY ZONING CHECK SET — OWNER-PREPARED, NOT FOR CONSTRUCTION

October 15, 2026 · Dimensions in feet-inches · Plan north = street side

Floor plan & areas **Z-2**

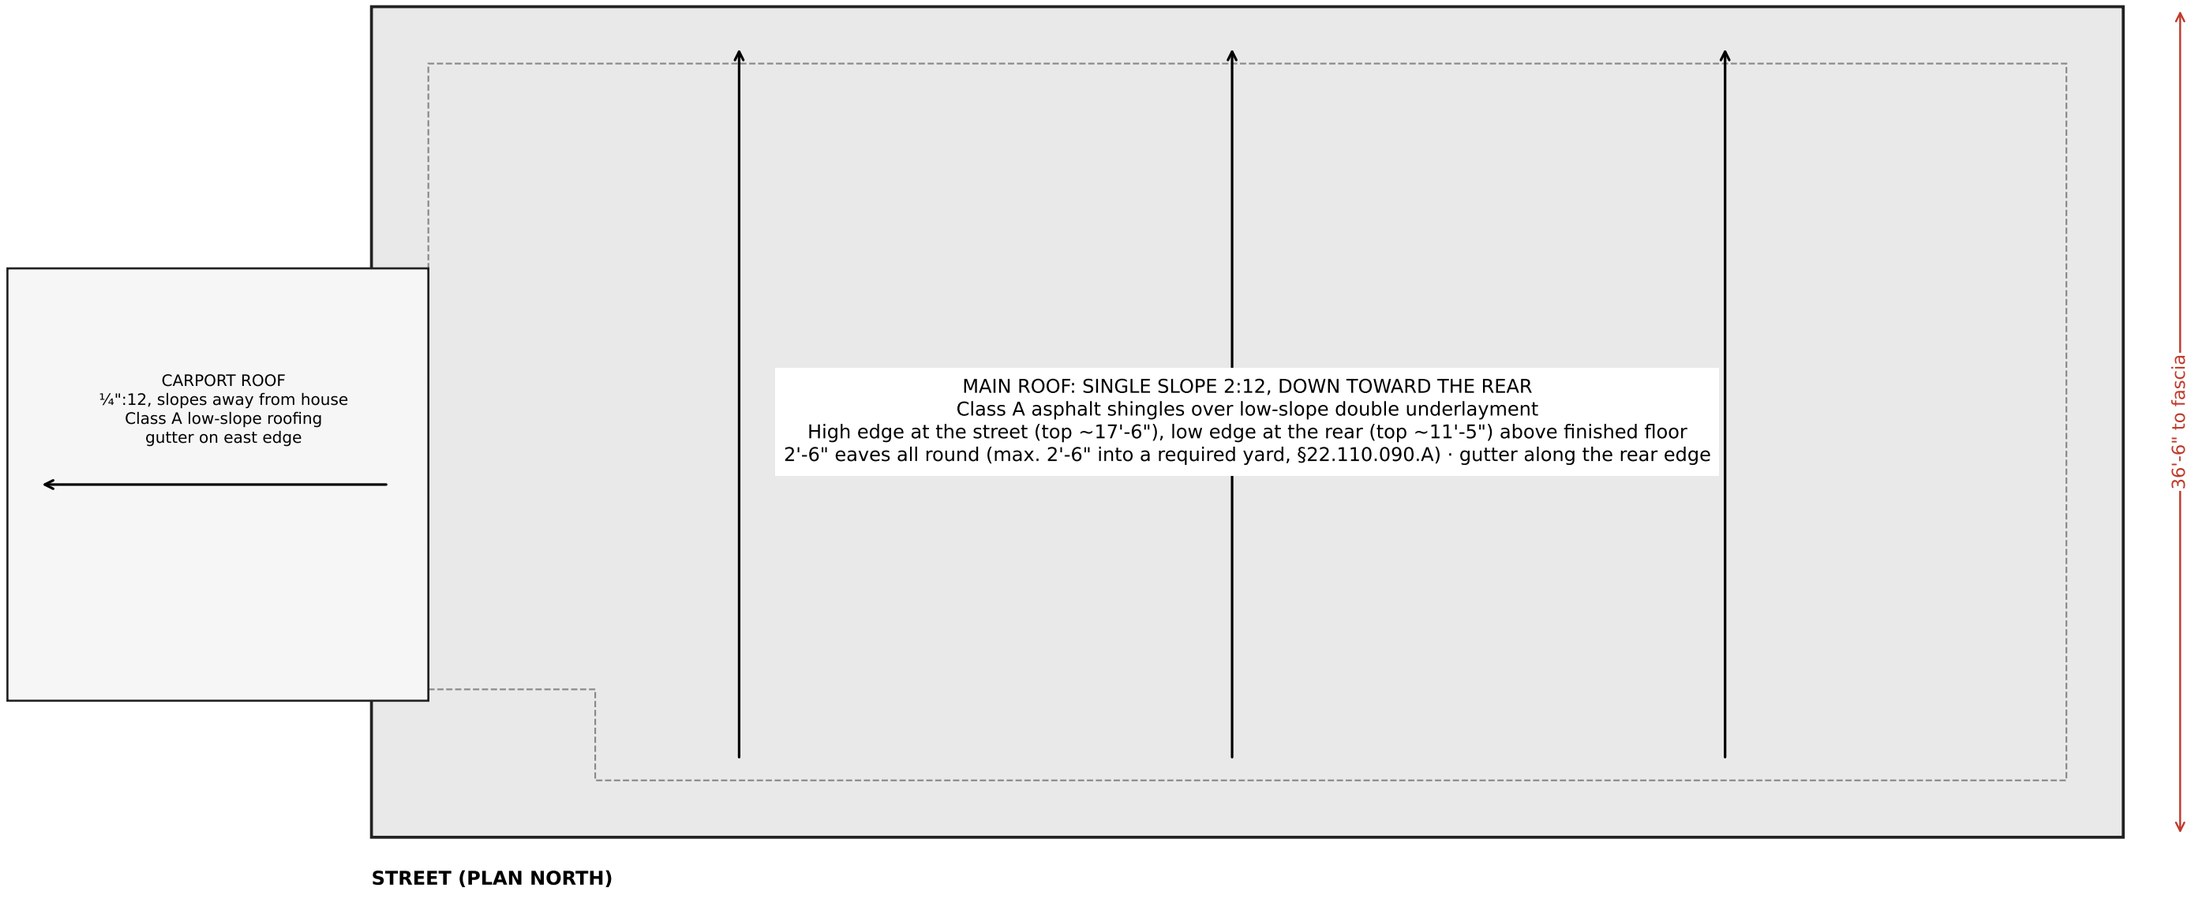

Single-family residence rebuild (Eaton Fire), 220 Laurel Dr, Altadena CA 91001

APN 5832-003-027 · Zone R-1, Altadena Community Standards District · Owner: Richard Acosta

PRELIMINARY ZONING CHECK SET — OWNER-PREPARED, NOT FOR CONSTRUCTION


October 15, 2026 · Dimensions in feet-inches · Plan north = street side

Roof plan **Z-3**


Heights above finished floor. The lot falls ~4' across the footprint (survey); grade lines and height above grade to follow the foundation/grading design.

Street facade articulation (§22.140.520, Table 22.140.520-C): (1) weather protection: flat metal canopies 3'-0" deep over 4 of the 5 street windows; (2) recessed windows: all street windows set 6" behind the stucco face.
Rear: matching canopies over the kitchen and primary bedroom windows.


NORTH (STREET) ELEVATION

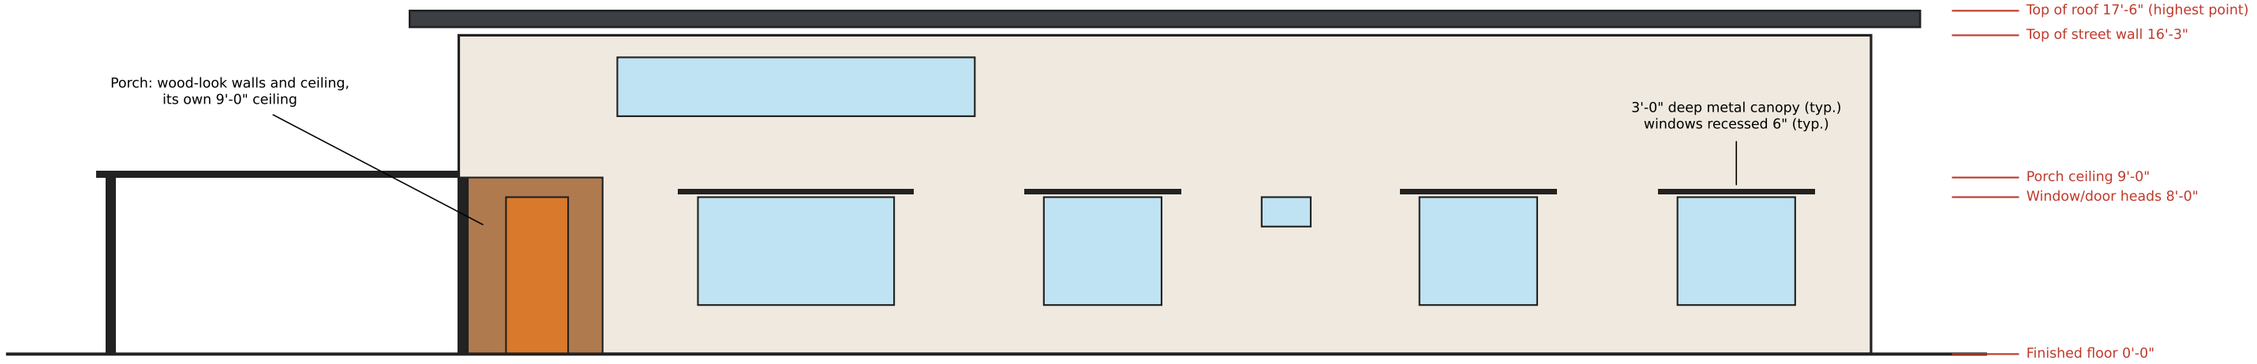


SOUTH (REAR) ELEVATION

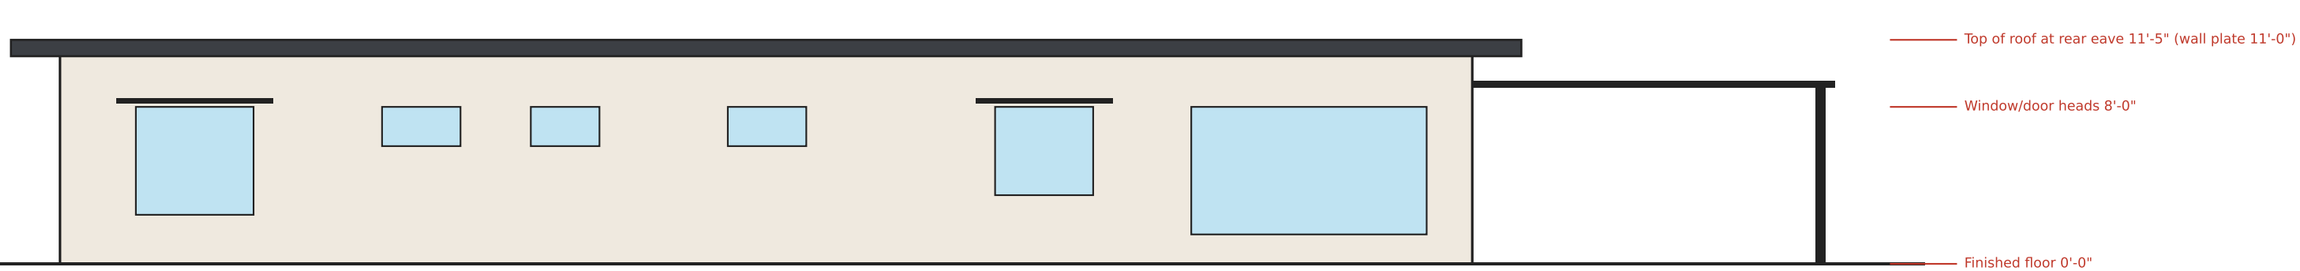

EAST (CARPORT) ELEVATION

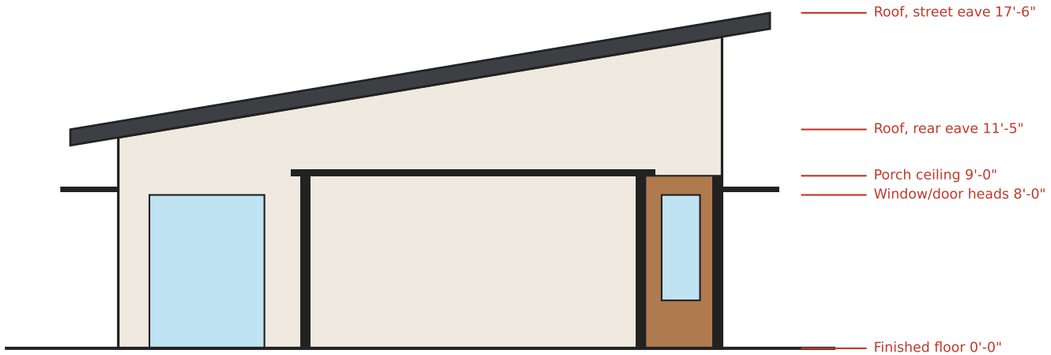

WEST ELEVATION

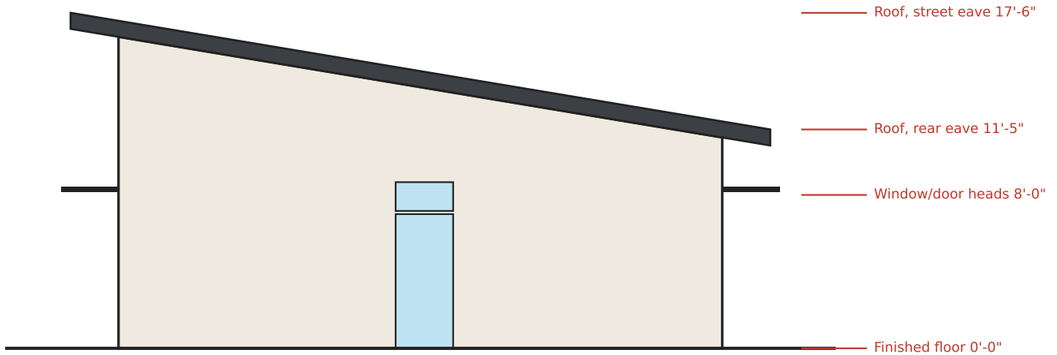

Single-family residence rebuild (Eaton Fire), 220 Laurel Dr, Altadena CA 91001

APN 5832-003-027 · Zone R-1, Altadena Community Standards District · Owner: Richard Acosta

PRELIMINARY ZONING CHECK SET — OWNER-PREPARED, NOT FOR CONSTRUCTION

October 15, 2026 · Dimensions in feet-inches · Plan north = street side