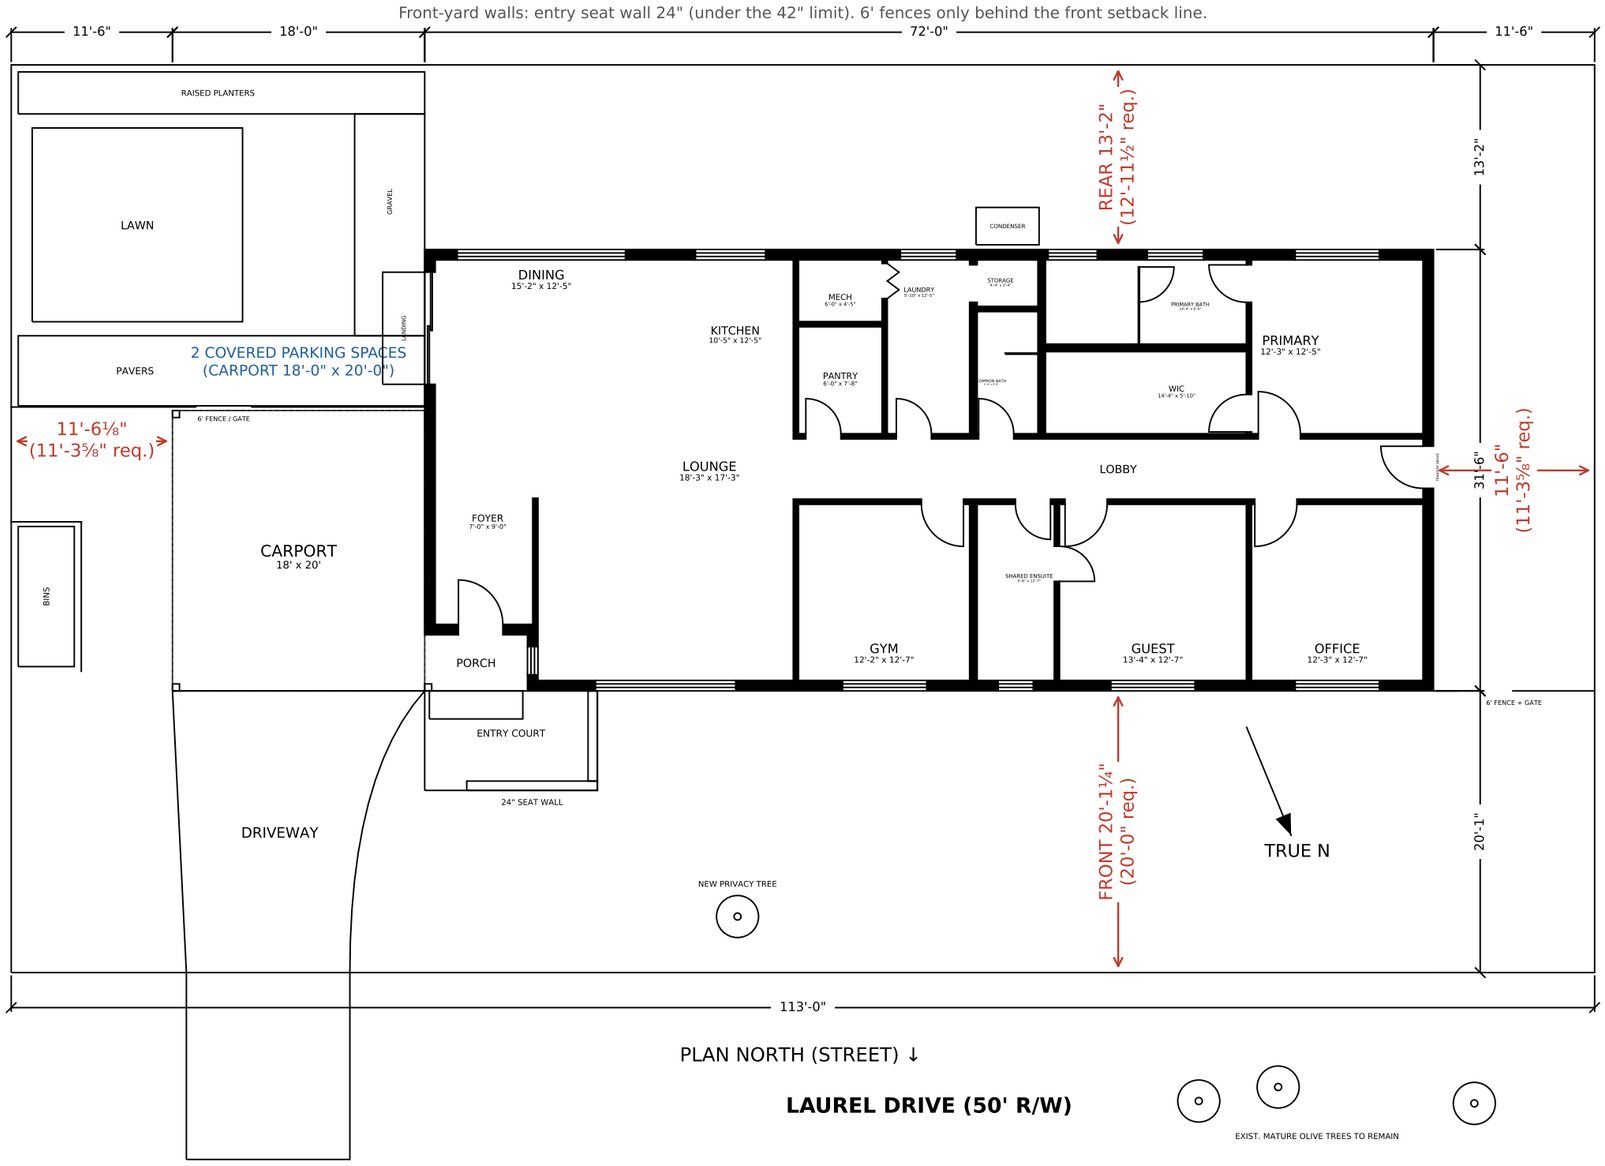




## PROJECT DATA

| | |
|---|---|
| Scope | Non-like-for-like rebuild, 1-story SFR + attached carport (Eaton Fire) |
| Zone / overlay | R-1 · Altadena CSD · VHFHSZ |
| Lot | 113.00' x 64.77' = 7,319 sq ft |
| Floor area (to outside of walls) | 2,238 sq ft |
| Covered porch | 29 sq ft |
| Carport (attached, open) | 360 sq ft |
| Lot coverage | 2,628 sq ft (35.9%) |
| CSD limit (¼ lot + 1,000) | 2,830 sq ft (coverage and floor area) |
| Stories / max height | 1 story · ~17'-7" above finished floor (top of roof at the street eave) |
| Bedrooms / baths | 4 / 3 |
| Parking | 2 covered (carport) |

| **SETBACKS** | required · provided |
|---|---|
| Front (street) | 20'-0" · 20'-1¼" |
| Rear | 12'-11½" · 13'-2" |
| Side, west | 11'-3⅝" · 11'-6" |
| Side, east (carport) | 11'-3⅝" · 11'-6⅛" |

| | |
|---|---|
| Glazing (Title 24 check) | ~448 sq ft (~20.0% of floor) |

NOTES
1. Setbacks measured to the outside face of exterior walls (eaves excluded).
2. Side setback taken as 10% of lot width; rear as 20% of lot depth. Please confirm.
3. Heights are above finished floor; the lot falls ~4' across the footprint, so height above grade depends on the foundation design (to be set with the civil).
4. Existing retaining wall and chimney (survey) to be removed.
5. Survey: topographic survey on file (APN above).

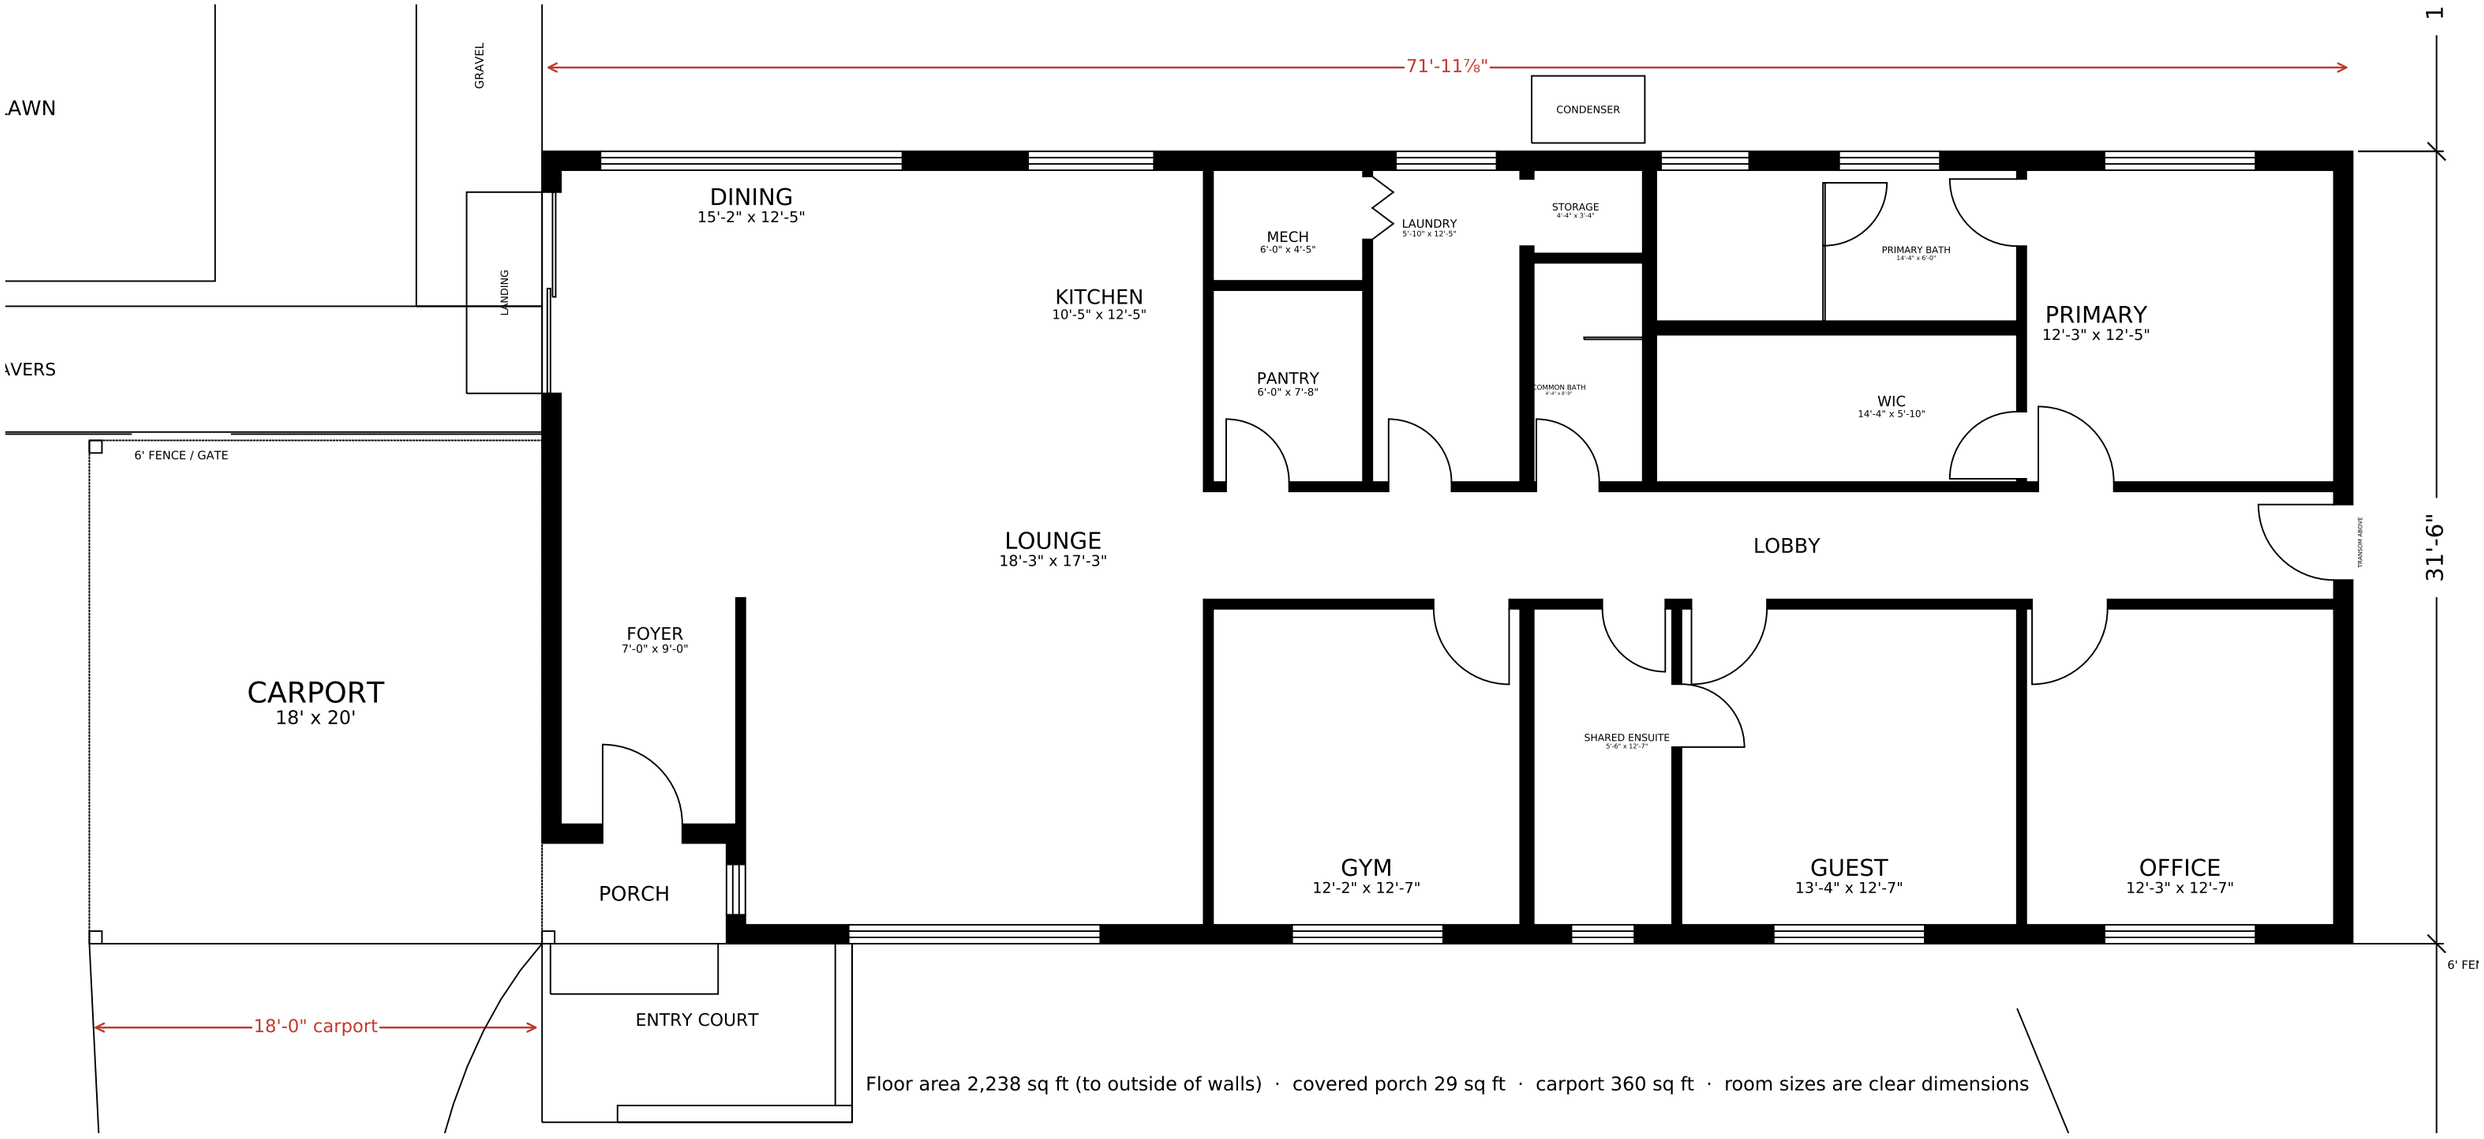


Floor area 2,238 sq ft (to outside of walls) · covered porch 29 sq ft · carport 360 sq ft · room sizes are clear dimensions


**Single-family residence rebuild (Eaton Fire), 220 Laurel Dr, Altadena CA 91001**

APN 5832-003-027 · Zone R-1, Altadena Community Standards District · Owner: Richard Acosta

PRELIMINARY ZONING CHECK SET — OWNER-PREPARED, NOT FOR CONSTRUCTION

October 15, 2026 · Dimensions in feet-inches · Plan north = street side

Floor plan & areas **Z-2**

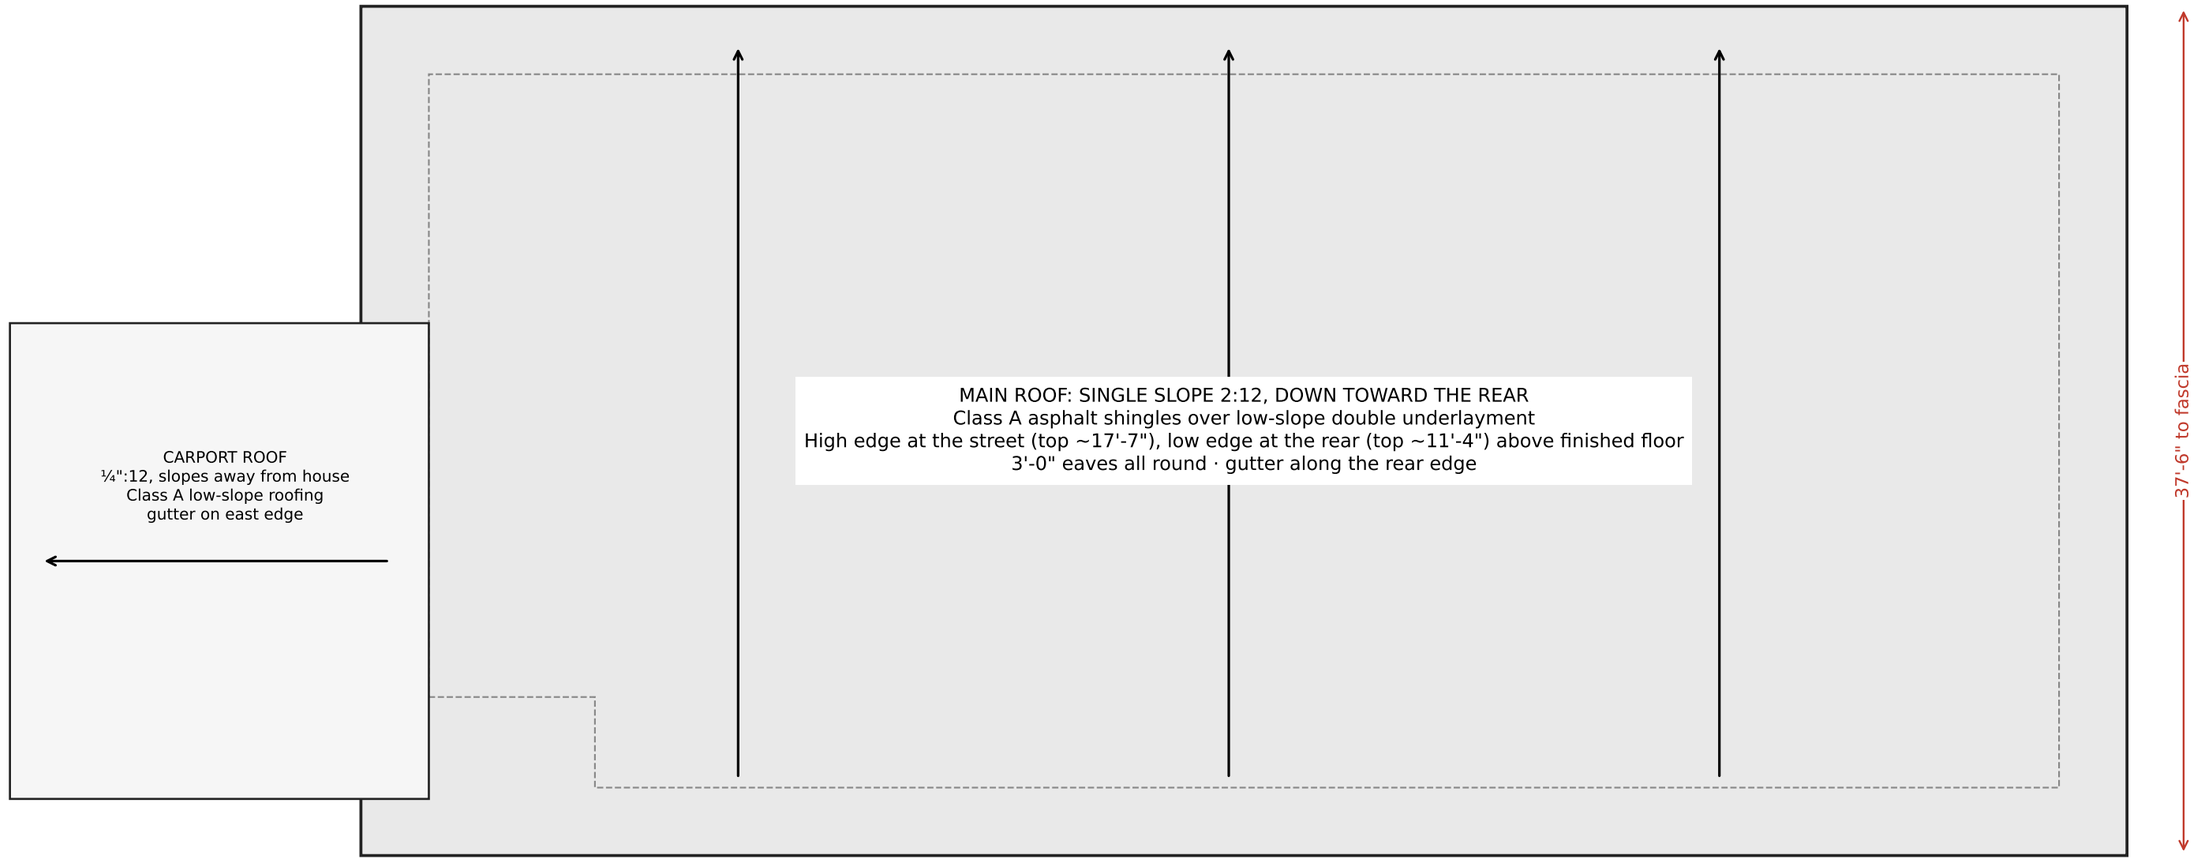


**Single-family residence rebuild (Eaton Fire), 220 Laurel Dr, Altadena CA 91001**

APN 5832-003-027 · Zone R-1, Altadena Community Standards District · Owner: Richard Acosta


PRELIMINARY ZONING CHECK SET — OWNER-PREPARED, NOT FOR CONSTRUCTION

October 15, 2026 · Dimensions in feet-inches · Plan north = street side


Roof plan **Z-3**

Heights above finished floor. The lot falls ~4' across the footprint (survey); grade lines and height above grade to follow the foundation/grading design.


## NORTH (STREET) ELEVATION

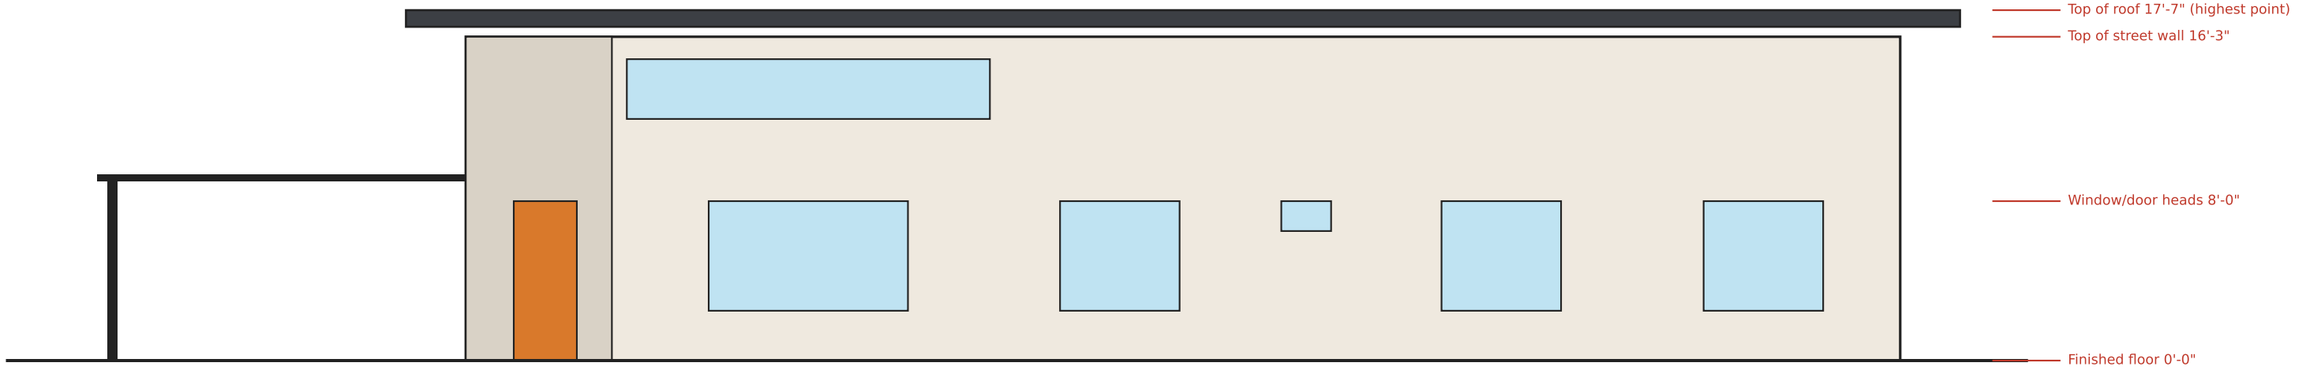


## SOUTH (REAR) ELEVATION

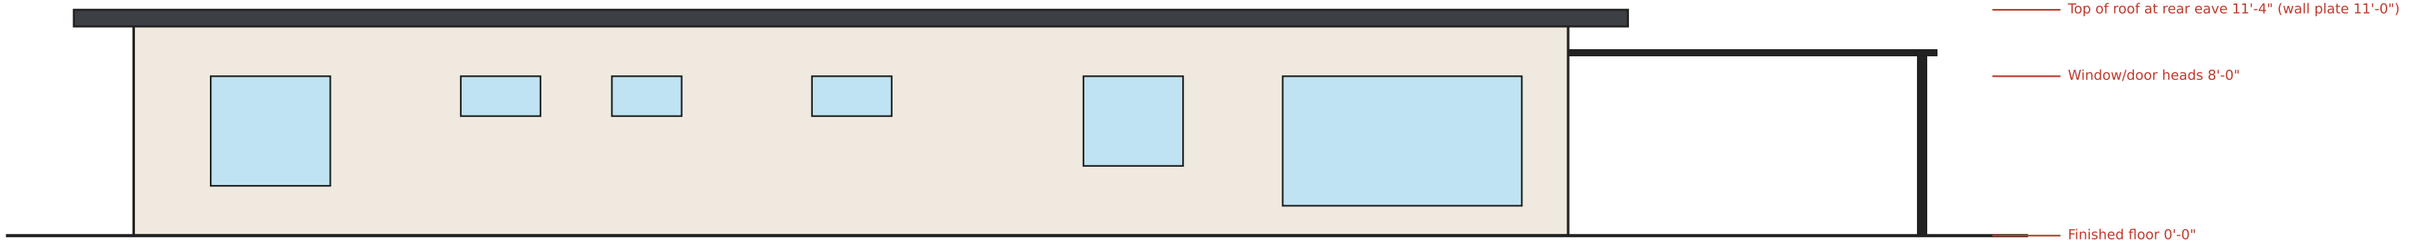


## EAST (CARPORT) ELEVATION

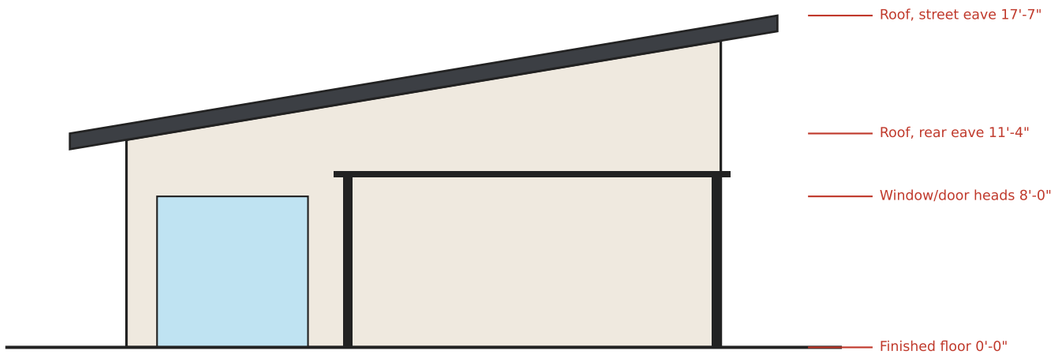


## WEST ELEVATION

